

Architect
OpeningDesign
312 W. Lakeside St.
Madison, WI 53715
Ryan
ryan@openingdesign.com
773-425-6456


openingdesign


Structural
ntrive
100 S. Ashland Ave., #82002
Chicago, IL 60608
Steven Uecke
s.uecke@ntrive.com
630-460-4120x101



NTRIVE

INNOVATIVE ENGINEERING

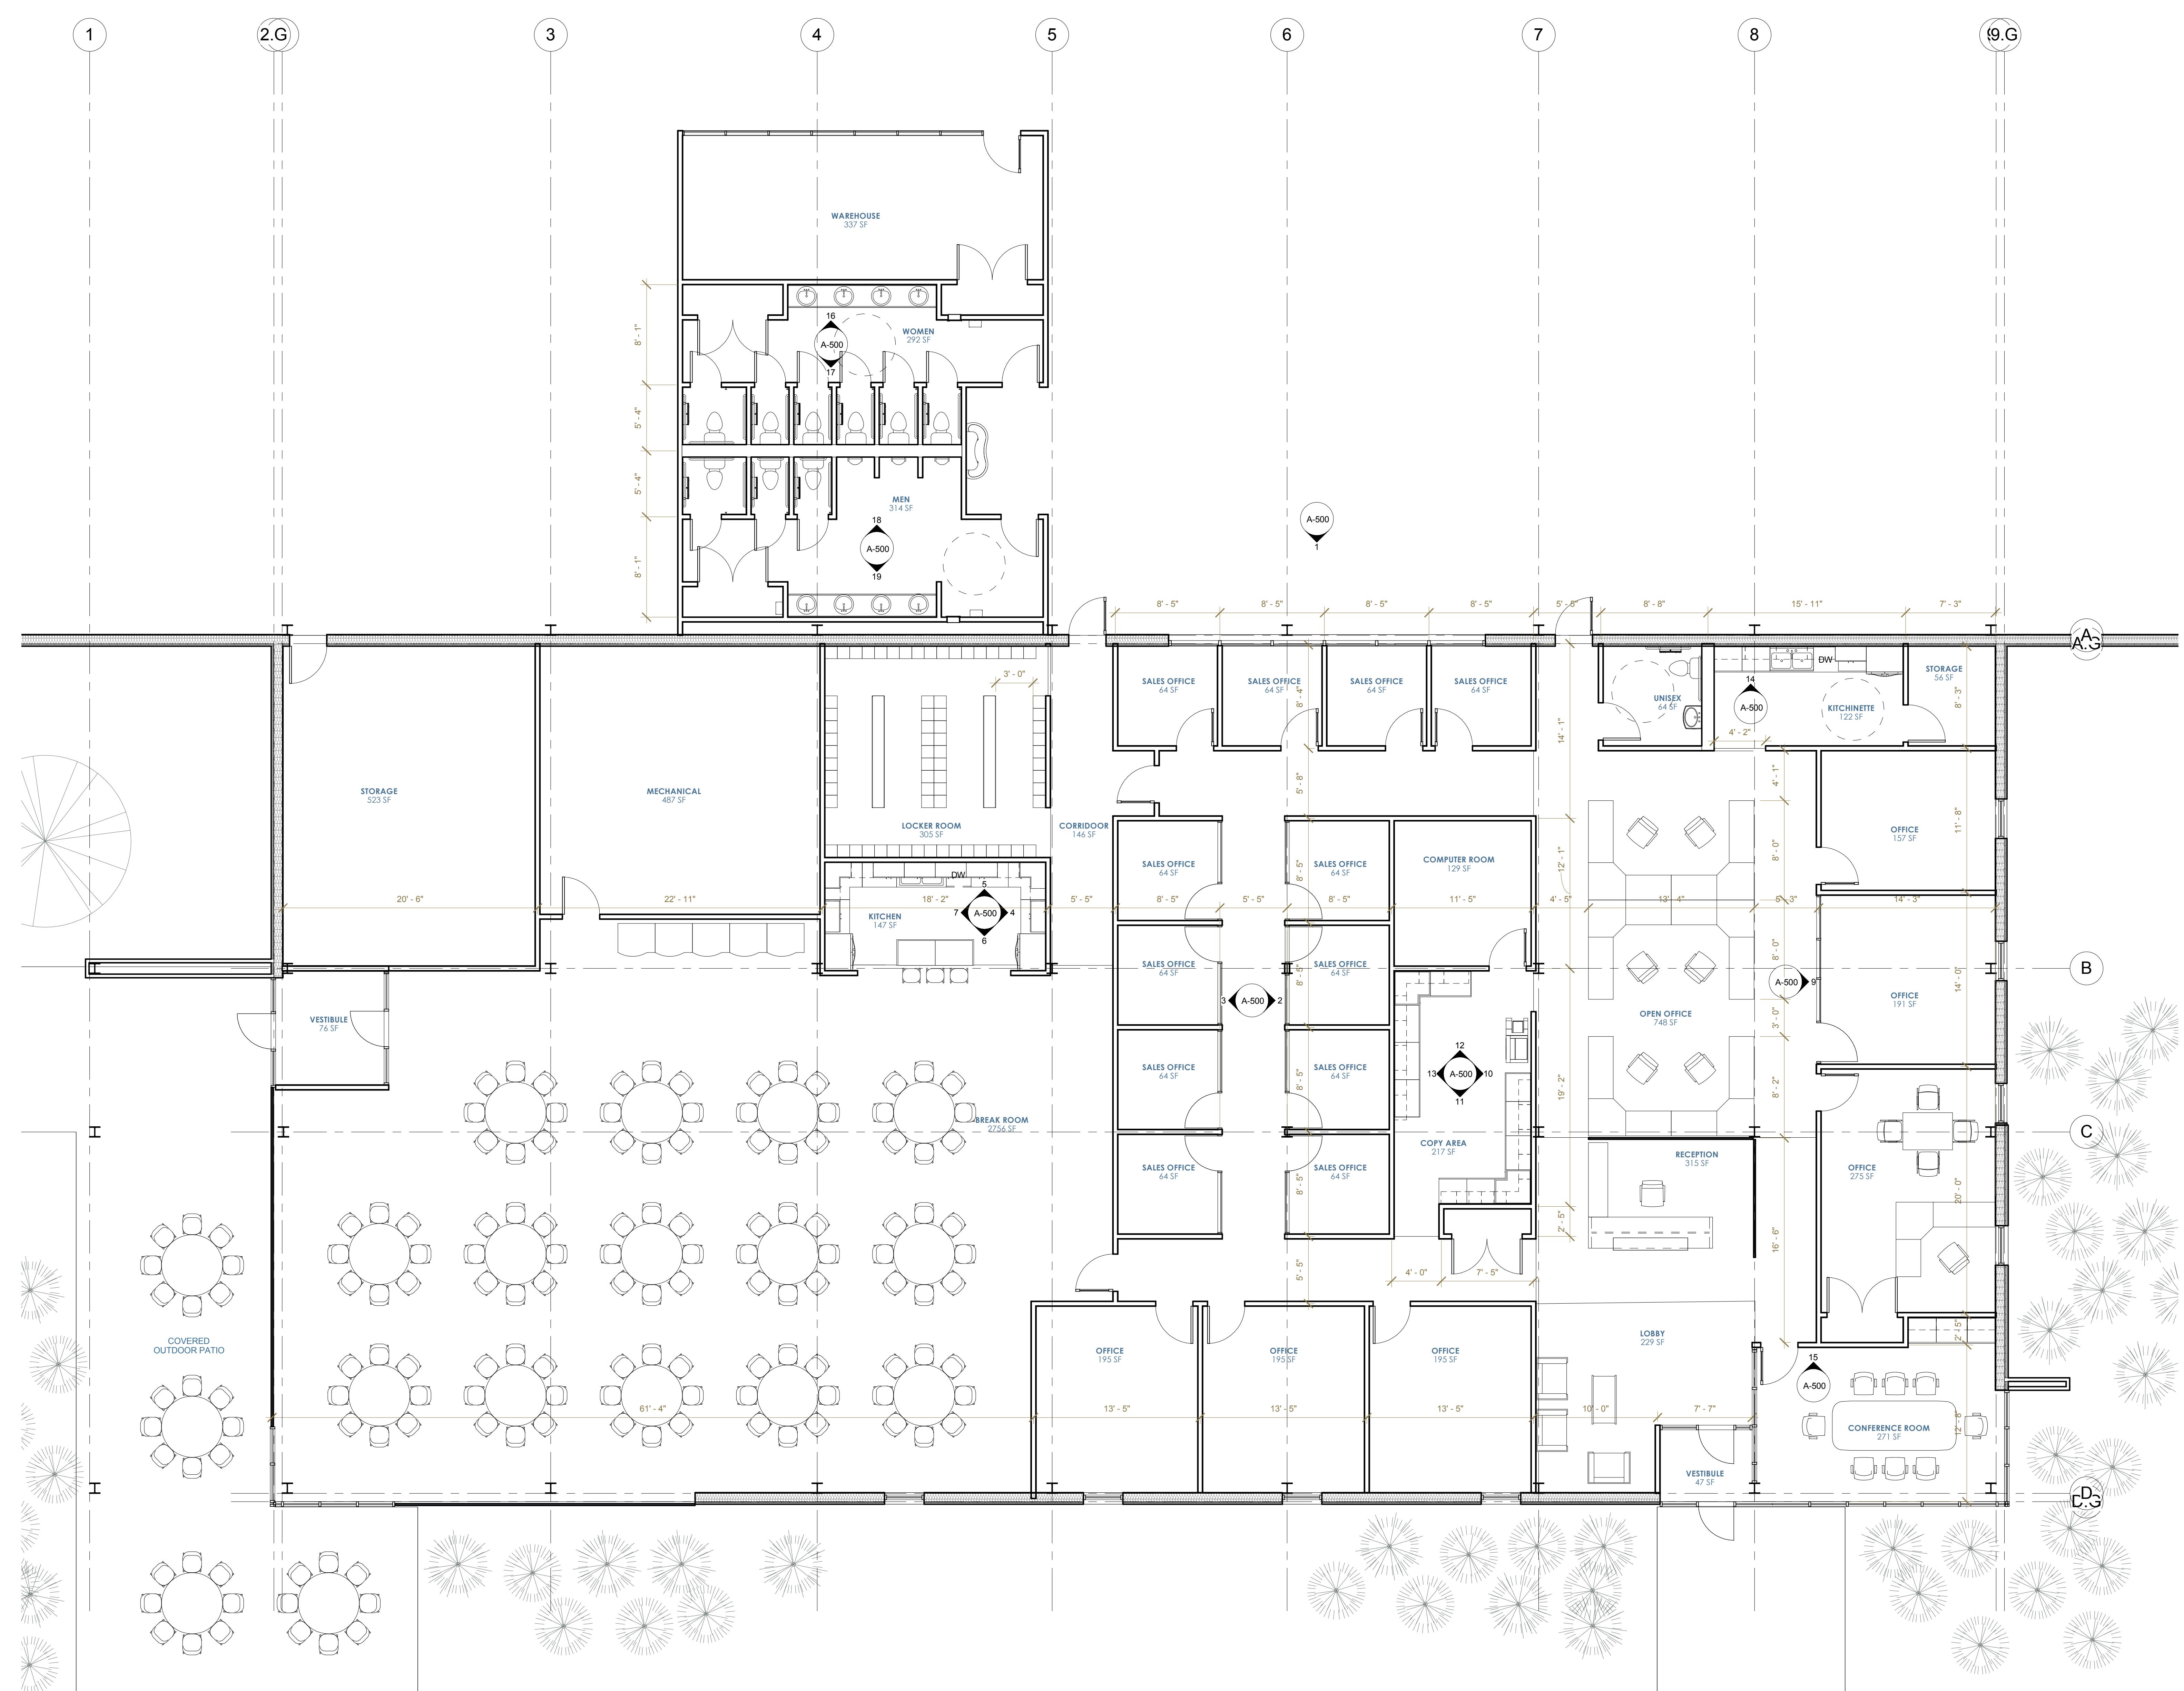


Open Source
Metal Building
FLOOR PLAN -
OFFICE ANNEX

Date 8/27/2015 9:50:29 AM

A-100

Scale

3/16" = 1'-0"

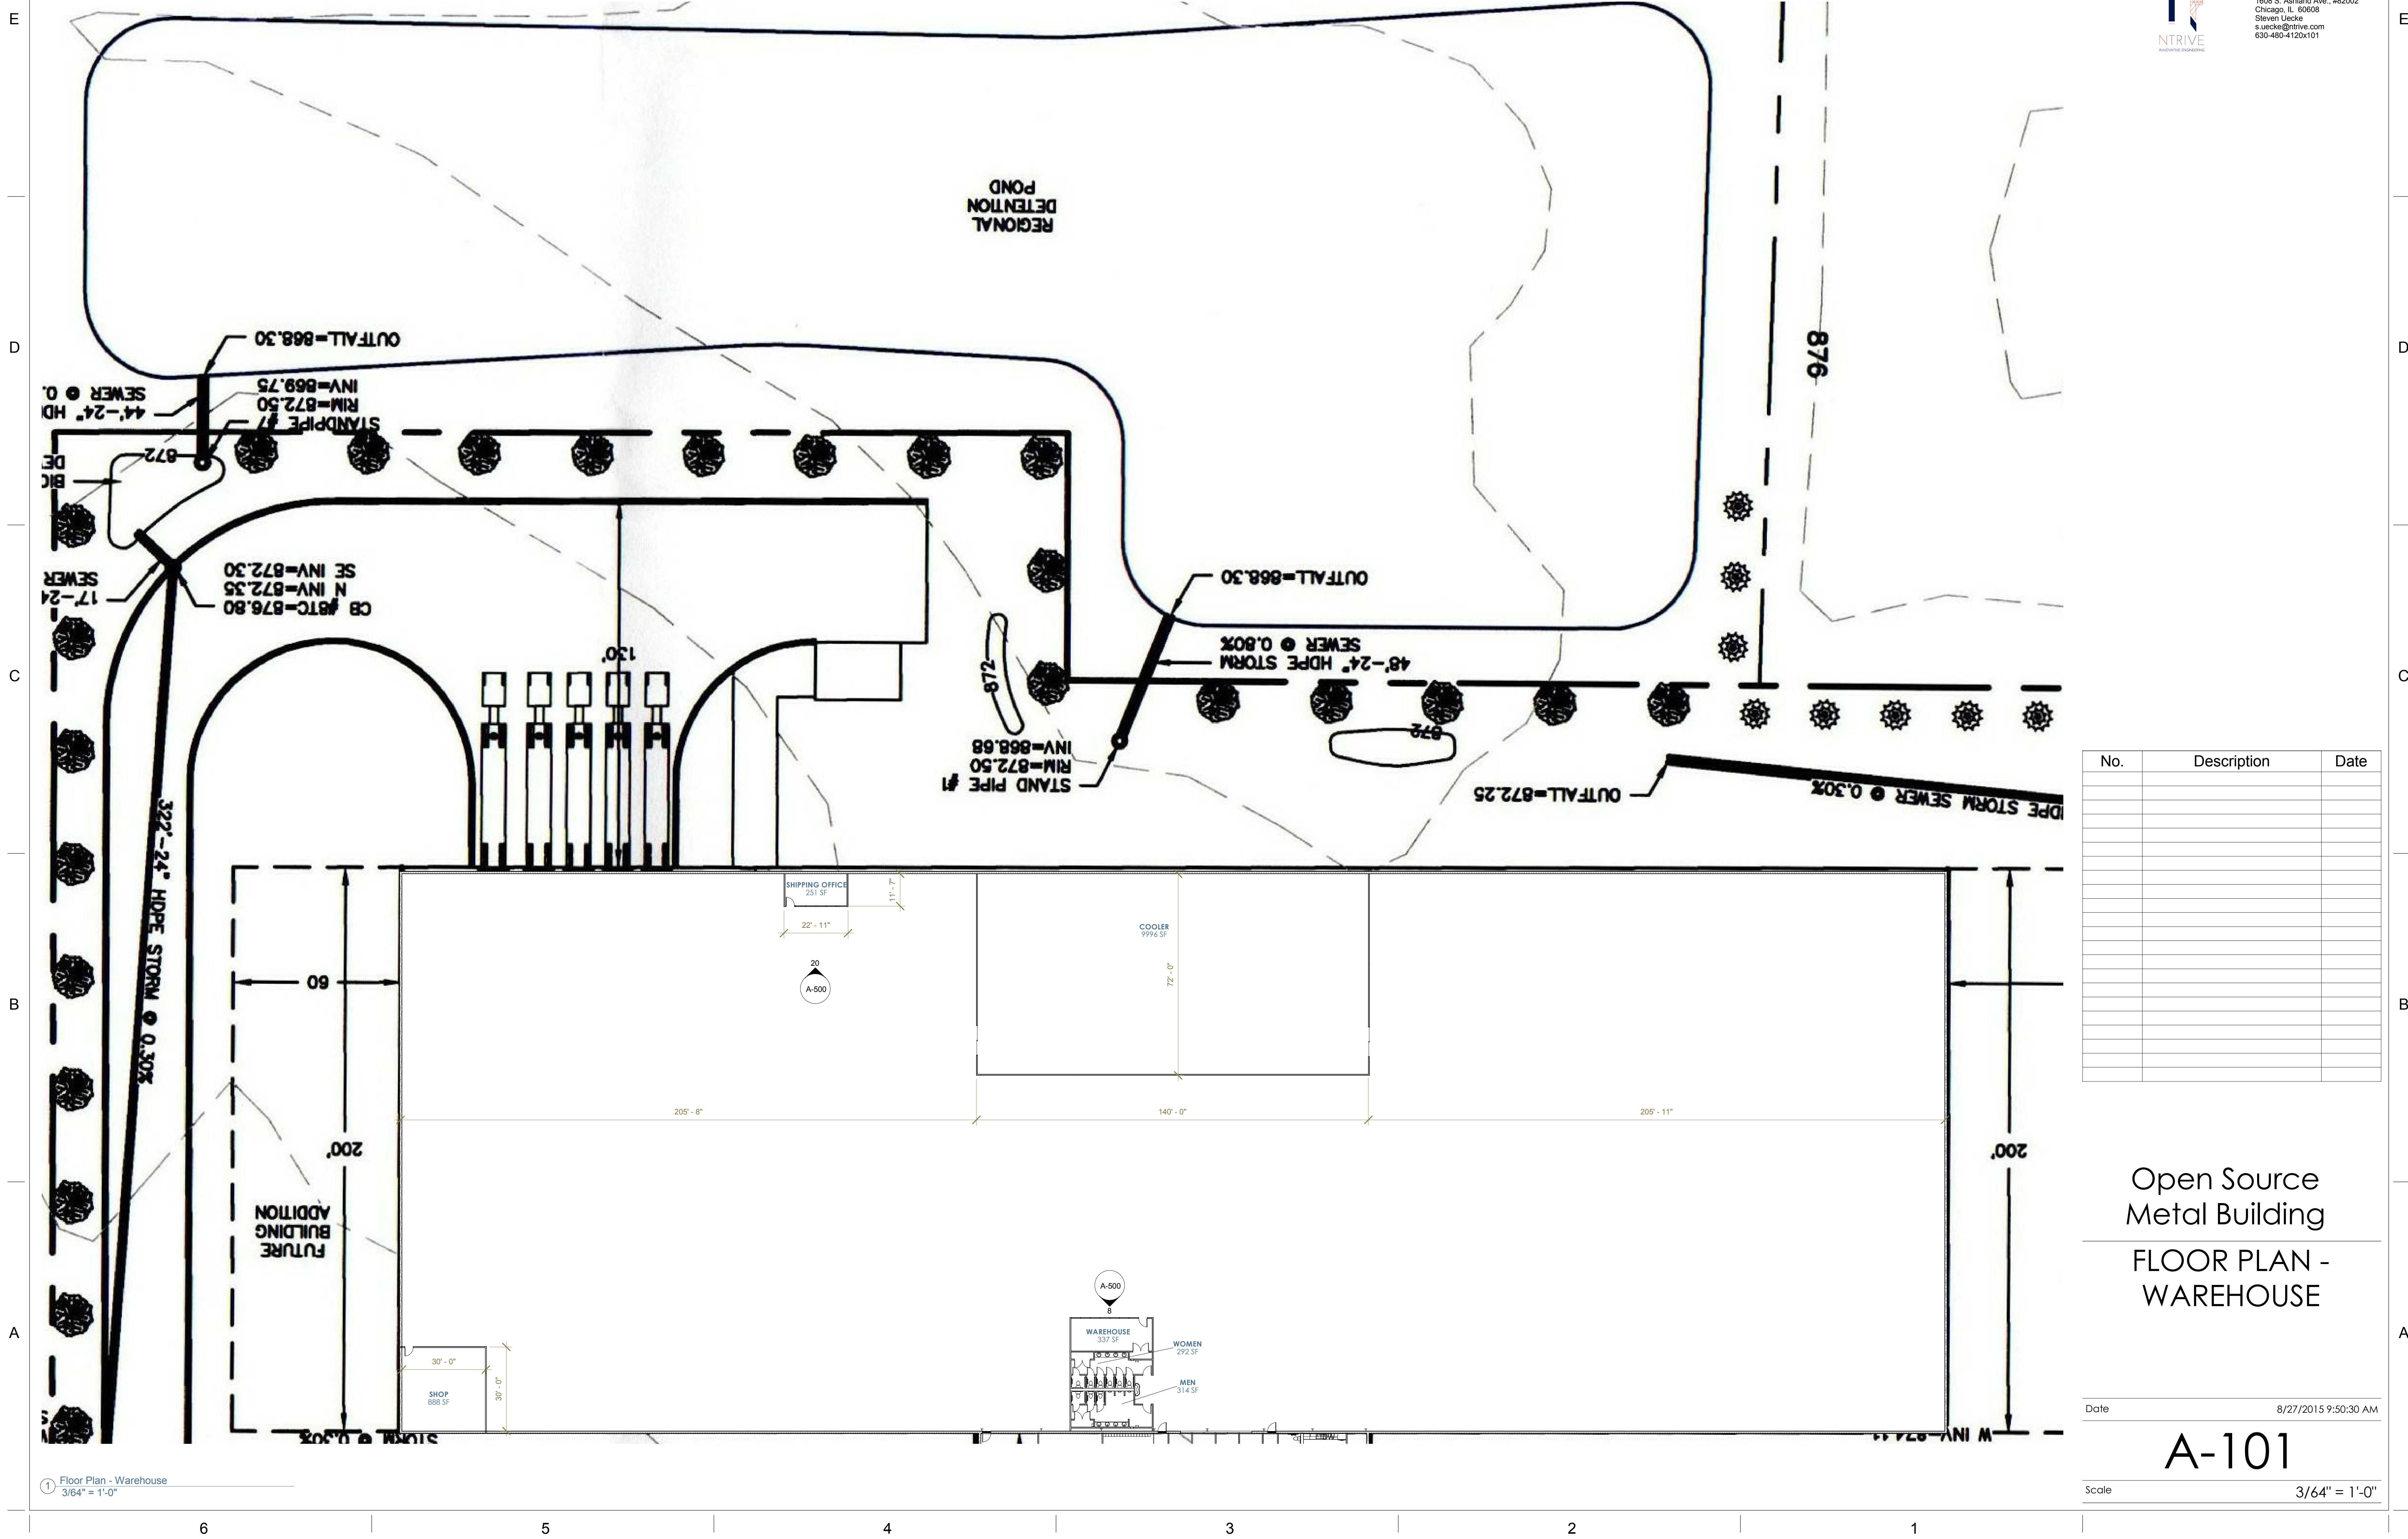



The logo for OpeningDesign features a stylized lowercase 'd' where the top loop contains a smaller 'o'. Below the 'd' is the word 'openingdesign' in a lowercase sans-serif font.

Structural
ntrive
1608 S. Ashland Ave., #82002
Chicago, IL 60608
Steven Uecke
s.uecke@ntrive.com
630-480-4120x101

Open Source Metal Building

REFLECTED CEILING PLAN - OFFICE ANNEX

Date 8/27/2015 9:50:33 AM

A-150

'16" = 1'-0"

REFLECTED CEILING PLAN - OFFICE ANNEX

nitect
n Design
W. Lakeside St
ison, WI 53715
n Schultz
[@openingdesign.com
425-6456](mailto:@openingdesign.com)

The logo consists of a stylized lowercase 'd' where the dot is replaced by a smaller circle.

cultural
e
3 S. Ashland Ave., #82002
ago, IL 60608
en Uecke
cke@ntrive.com
480-4120x101

E

E

D

D

C

C

B

B


A

A

6

5

4

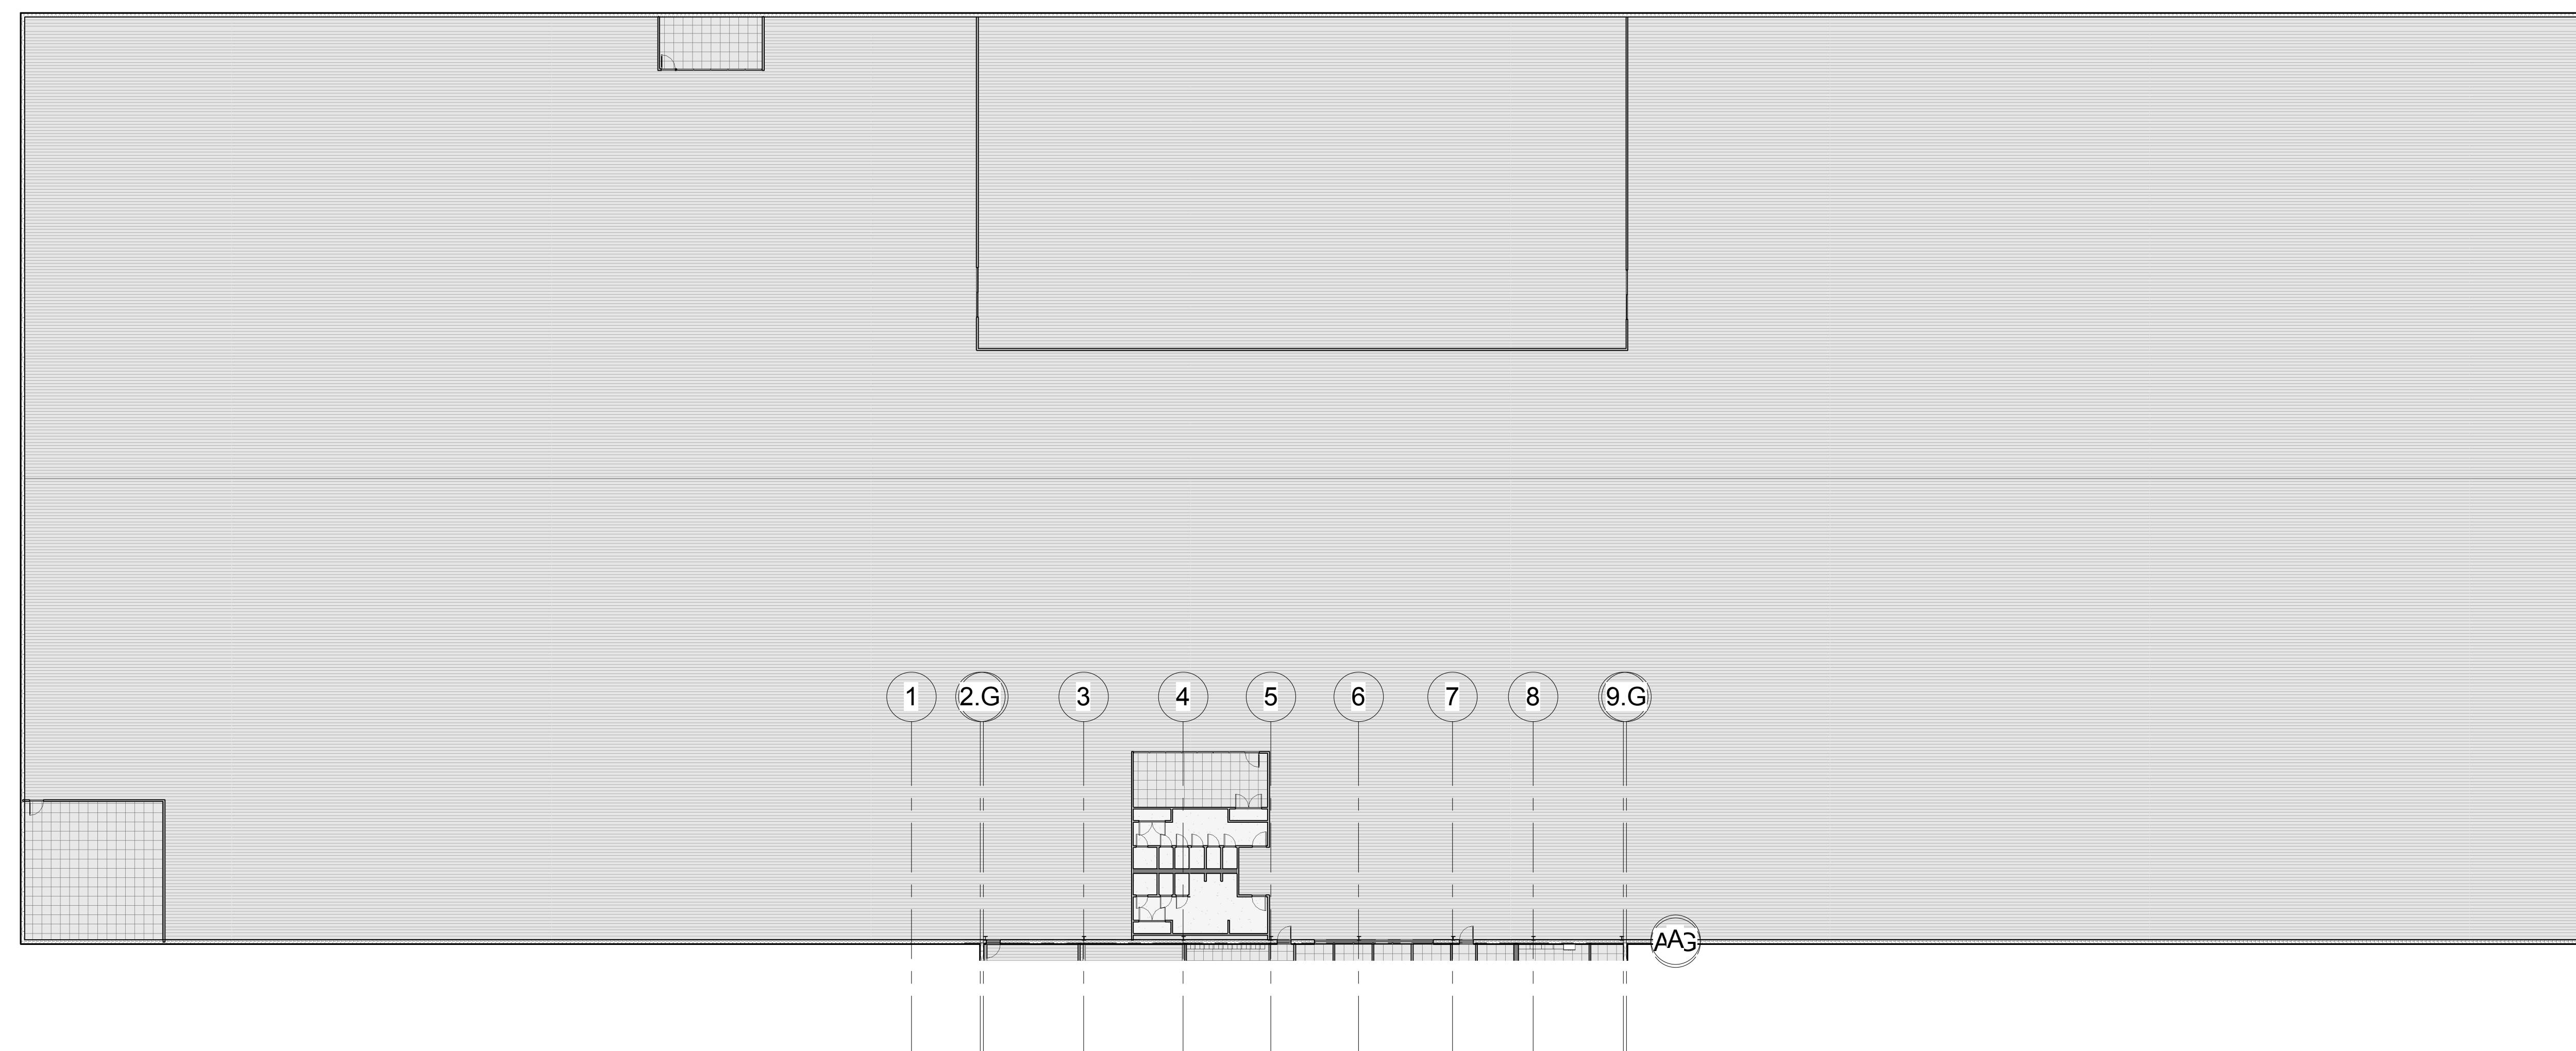

Open Source Metal Building

REFLECTED CEILING PLAN - WAREHOUSE

Date 8/27/2015 9:50:35 AM

A-151

6 | 5 | 4 | 3 | 2 | 1 |



ect
ngDesign
W. Lakeside St
on, WI 53715"
Schultz
[Openingdesign.com](http://openingdesign.com)
25-6456



S. Ashland Ave., #82002
go, IL 60608
n Uecke
uecke@ntrive.com
80-4120x101

E

An architectural rendering of a modern building's exterior. The building features a long, horizontal grey wall with vertical cladding. A series of dark grey rectangular panels are attached to the right side of this wall, creating a textured pattern. Below the main wall, there is a lower section with large glass windows. To the left of these windows, there is a white wall with horizontal slats and a small balcony area where two people are standing. To the right of the windows, there are more vertical panels and a set of double doors. The ground in front of the building is covered in green grass and small bushes. The sky above is a uniform light blue.

6D Building Elevation - North

C

This architectural rendering illustrates a modern building's exterior and interior. The building features a light grey horizontal corrugated panel system with perforations. A storefront with integrated glazing is shown, along with multi-wall insulation panels. The interior is visible through large glass windows, showing a dining or seating area with several people. The roofline is flat, and the overall design is clean and contemporary.

HORZ. CORRUGATED
PANEL - PERFORATED

MULTI-WALL INSUL.
POLYCARBONATE

STOREFRONT WITH IN
GLAZING

6B Building Elevation - East
3/16" = 1'-0"

B

An architectural rendering of a modern building complex. The main building features a dark grey facade with large windows and a prominent cantilevered section. To the right is a long, low-profile building with horizontal grey slats. In the foreground, there's a green lawn and a small white figure for scale. The sky is light blue with some clouds.

6A Building Elevation - West
3/16" = 1'-0"

Open Source Metal Building Exterior Elevations

Date 8/27/2015 9:52:34 AM

A-300

Scale 3/16" = 1'-0"

uct
ngDesign
/ Lakeside St
on, WI 53715"
Schultz
openingdesign.com
25-6456

S. Ashland Ave., #82002
Chicago, IL 60608
John Uecke
uecke@ntrive.com
80-4120x101



1 Exterior - Main Entry

2 Exterior - Breakroom Entry



3 Interior - Breakroom

4 Interior - Open Office

5 Exterior - Main Entry Copy 1

Open Source Metal Building PERSPECTIVES

Date 8/27/2015 9:53:41 AM

A-900

Scale



ect
ngDesign
/ Lakeside St
on, WI 53715"
Schultz
openingdesign.com
25-6456



ultural
S. Ashland Ave., #82002
go, IL 60608
n Uecke
ke@ntrive.com
80-4120x101

Open Source Metal Building

INTERIOR ELEVATIONS

te 8/27/2015 9:50:42 AM

A-500

ale 1/4" = 1'-0"

