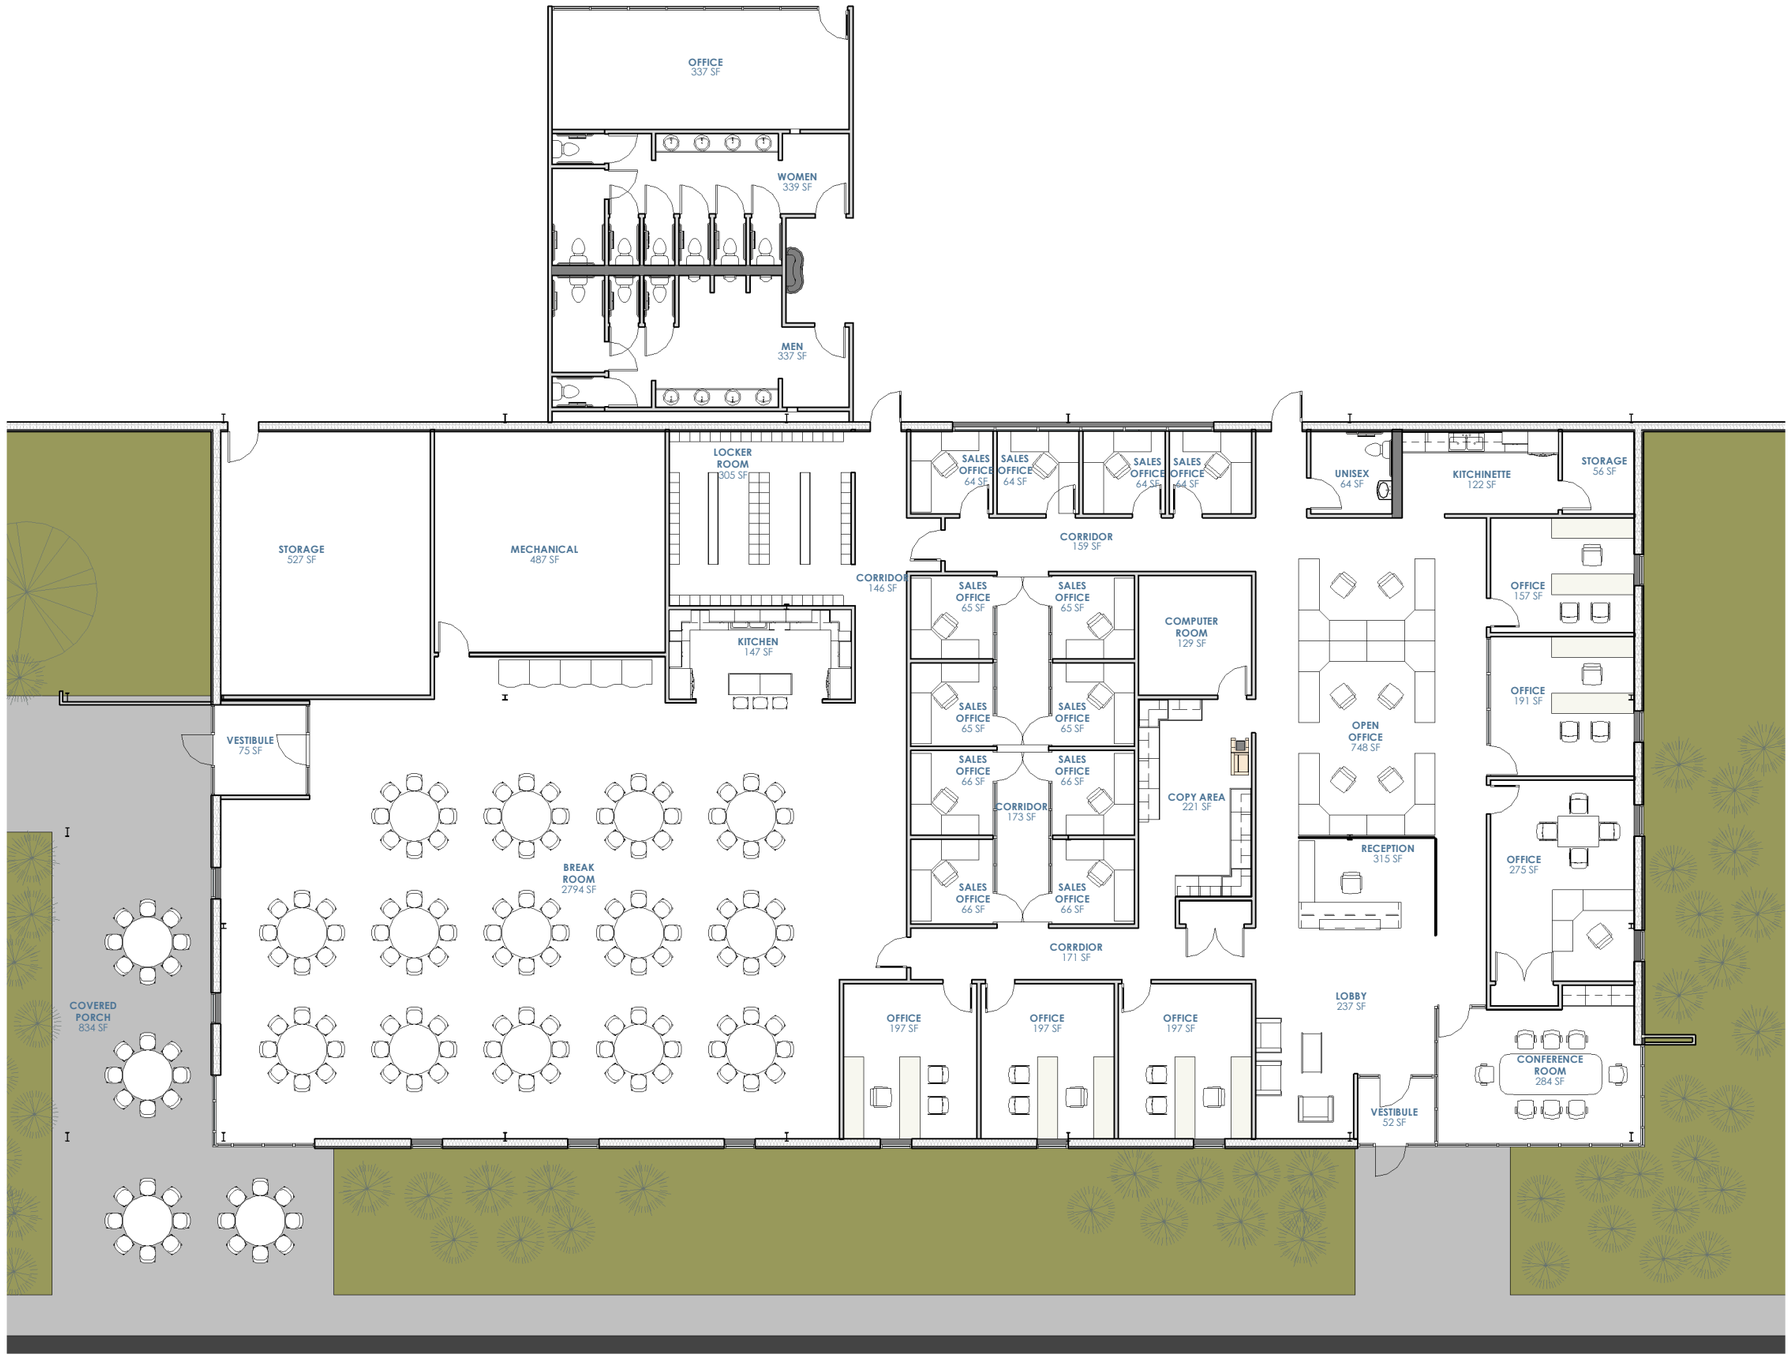
OFFICE
337 SF
WOMEN
339 SF
MEN
337 SF
STORAGE
527 SF
MECHANICAL
487 SF
LOCKER
ROOM
305 SF
KITCHEN
147 SF
VESTIBULE
75 SF
BREAK
ROOM
2794 SF
COVERED
PORCH
834 SF
SALES
OFFICE
64 SF
SALES
OFFICE
64 SF
SALES
OFFICE
64 SF
SALES
OFFICE
64 SF
CORRIDOR
159 SF
CORRIDOR
146 SF
SALES
OFFICE
65 SF
SALES
OFFICE
65 SF
SALES
OFFICE
65 SF
SALES
OFFICE
65 SF
SALES
OFFICE
66 SF
SALES
OFFICE
66 SF
CORRIDOR
173 SF
SALES
OFFICE
66 SF
SALES
OFFICE
66 SF
CORRDIOR
171 SF
COMPUTER
ROOM
129 SF
COPY AREA
221 SF
OFFICE
197 SF
OFFICE
197 SF
OFFICE
197 SF
UNISEX
64 SF
KITCHINETTE
122 SF
STORAGE
56 SF
OPEN
OFFICE
748 SF
RECEPTION
315 SF
LOBBY
237 SF
VESTIBULE
52 SF
OFFICE
157 SF
OFFICE
191 SF
OFFICE
275 SF
CONFERENCE
ROOM
284 SF

SHIPPING OFFICE 239 SF
COOLER 10020 SF
WAREHOUSE 96850 SF
SHOP 900 SF
OFFICE 337 SF
WOMEN 339 SF
MEN 337 SF
STORAGE 527 SF
MECHANICAL 487 SF
LOCKER ROOM 305 SF
KITCHEN 147 SF
BREAK ROOM 2794 SF
COVERED PORCH 834 SF
SALES OFFICE 64 SF
SALES OFFICE 64 SF
SALES OFFICE 64 SF
SALES OFFICE 64 SF
UNISEX 64 SF
KITCHINETTE 122 SF
STORAGE 56 SF
SALES OFFICE 65 SF
SALES OFFICE 65 SF
SALES OFFICE 65 SF
SALES OFFICE 65 SF
SALES OFFICE 66 SF
SALES OFFICE 66 SF
SALES OFFICE 66 SF
SALES OFFICE 66 SF
COMPUTER ROOM 129 SF
COPY AREA 221 SF
OPEN OFFICE 748 SF
RECEPTION 315 SF
LOBBY 237 SF
OFFICE 197 SF
OFFICE 197 SF
OFFICE 197 SF
CONFERENCE ROOM 284 SF
OFFICE 157 SF
OFFICE 191 SF
OFFICE 275 SF

HORZ. CORRUGATED METAL PANEL
PERFORATED HORZ. CORRUGATED METAL PANEL
STOREFRONT WITH INSULATED GLAZING

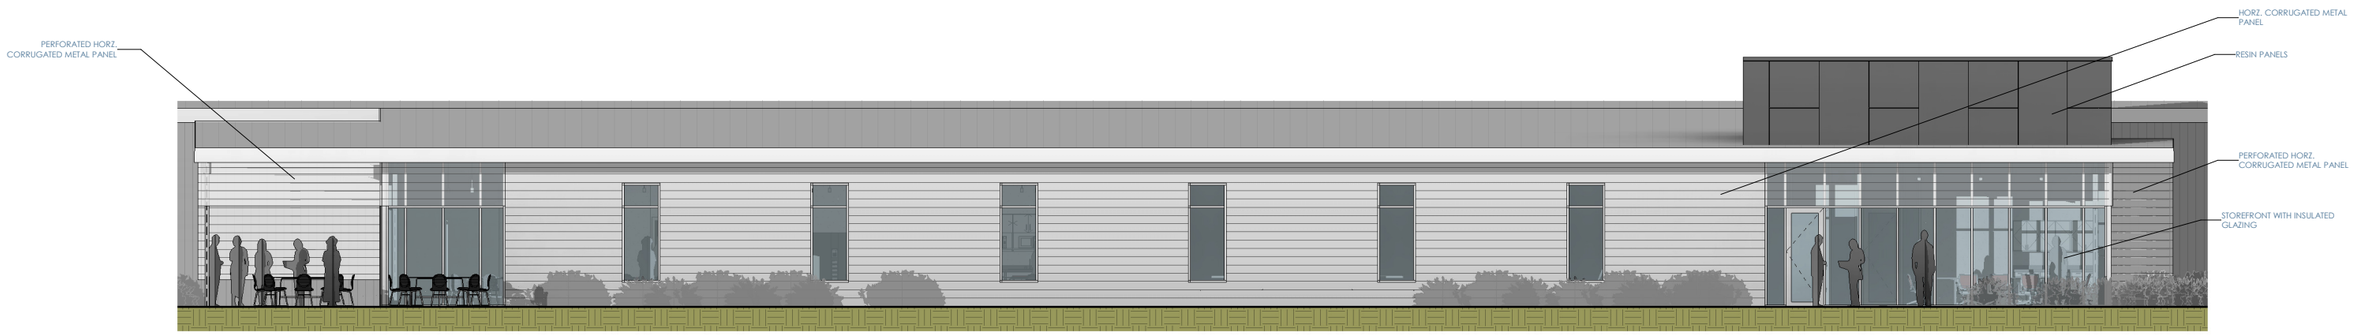
PERFORATED HORZ. CORRUGATED METAL PANEL
HORZ. CORRUGATED METAL PANEL
RESIN PANELS
PERFORATED HORZ. CORRUGATED METAL PANEL
STOREFRONT WITH INSULATED GLAZING

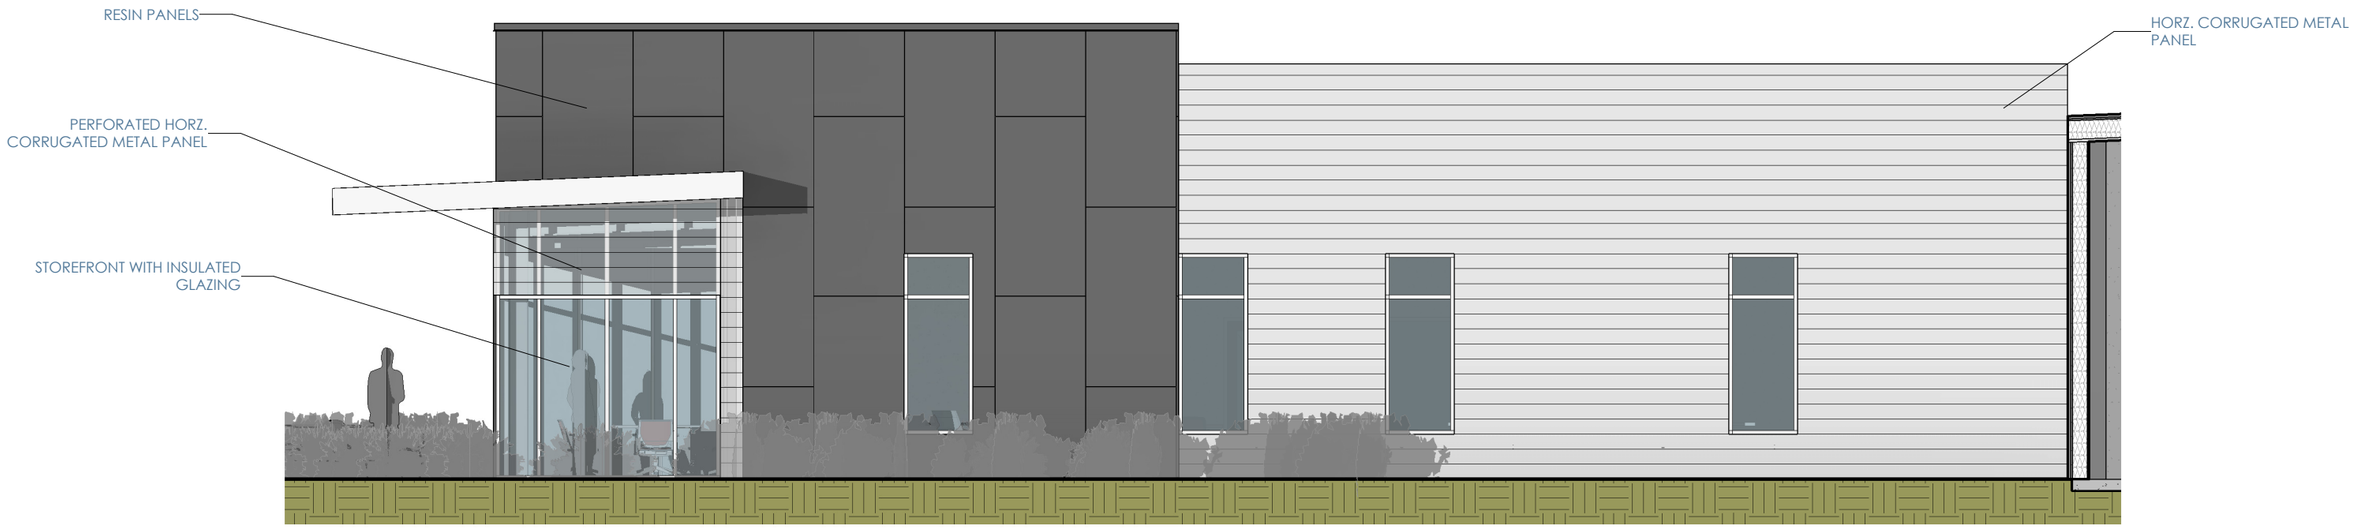
RESIN PANELS
PERFORATED HORZ. CORRUGATED METAL PANEL
STOREFRONT WITH INSULATED GLAZING
HORZ. CORRUGATED METAL PANEL

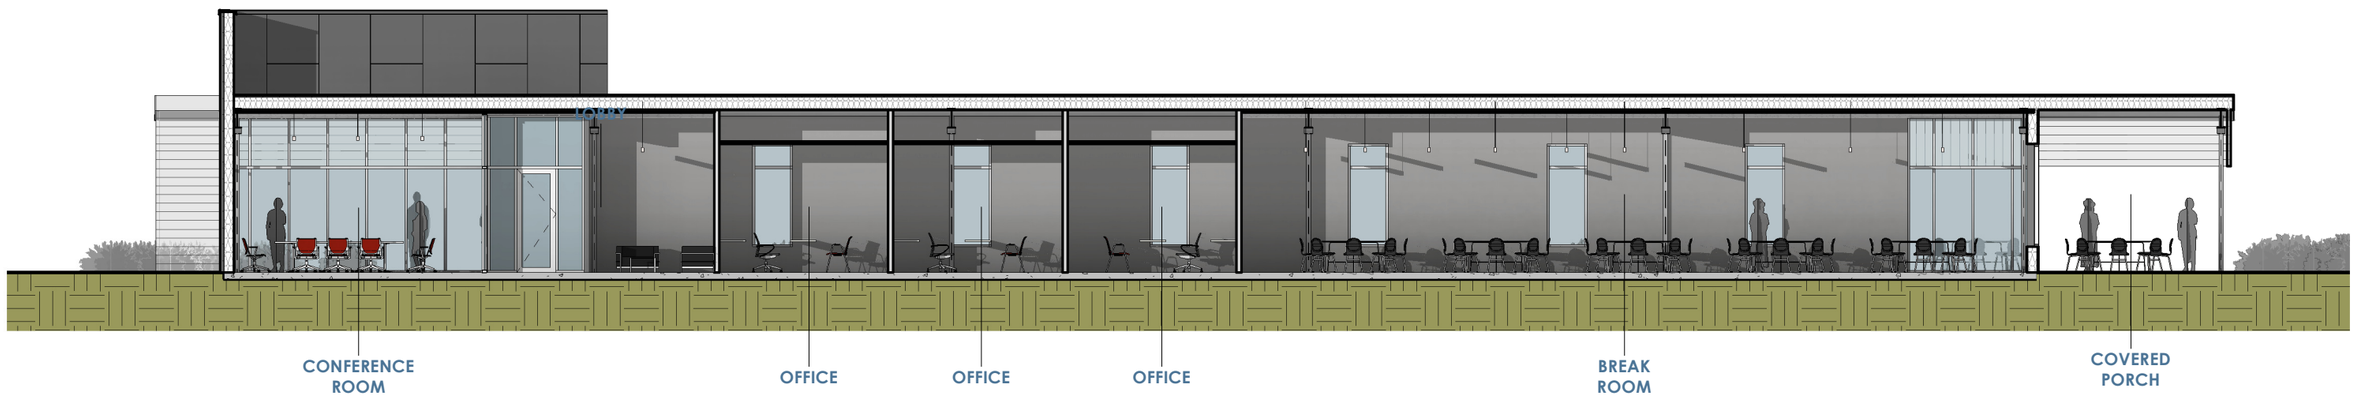
LOBBY
CONFERENCE ROOM
OFFICE
OFFICE
OFFICE
BREAK ROOM
COVERED PORCH

COVERED PORCH
BREAK ROOM
SALES OFFICE
SALES OFFICE
COPY AREA
OPEN OFFICE
OFFICE

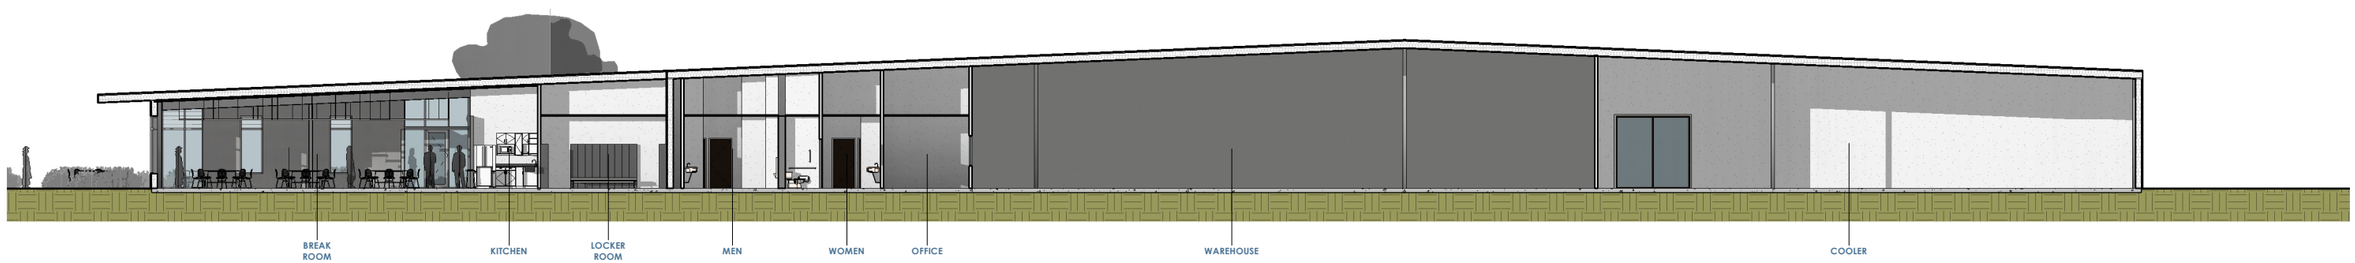
BREAK ROOM
KITCHEN
LOCKER ROOM
MEN
WOMEN
OFFICE
WAREHOUSE
COOLER

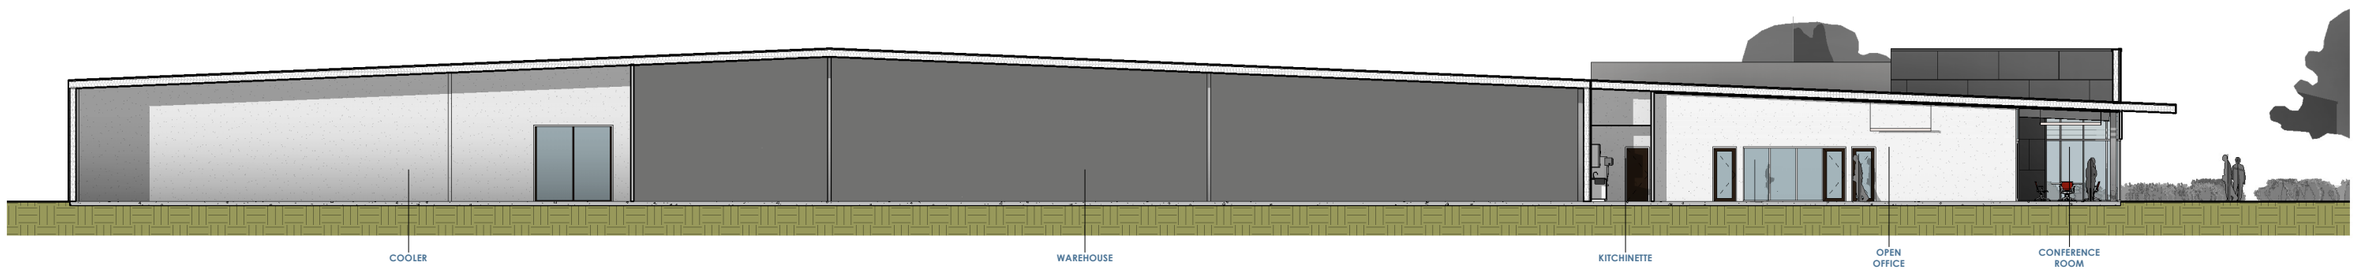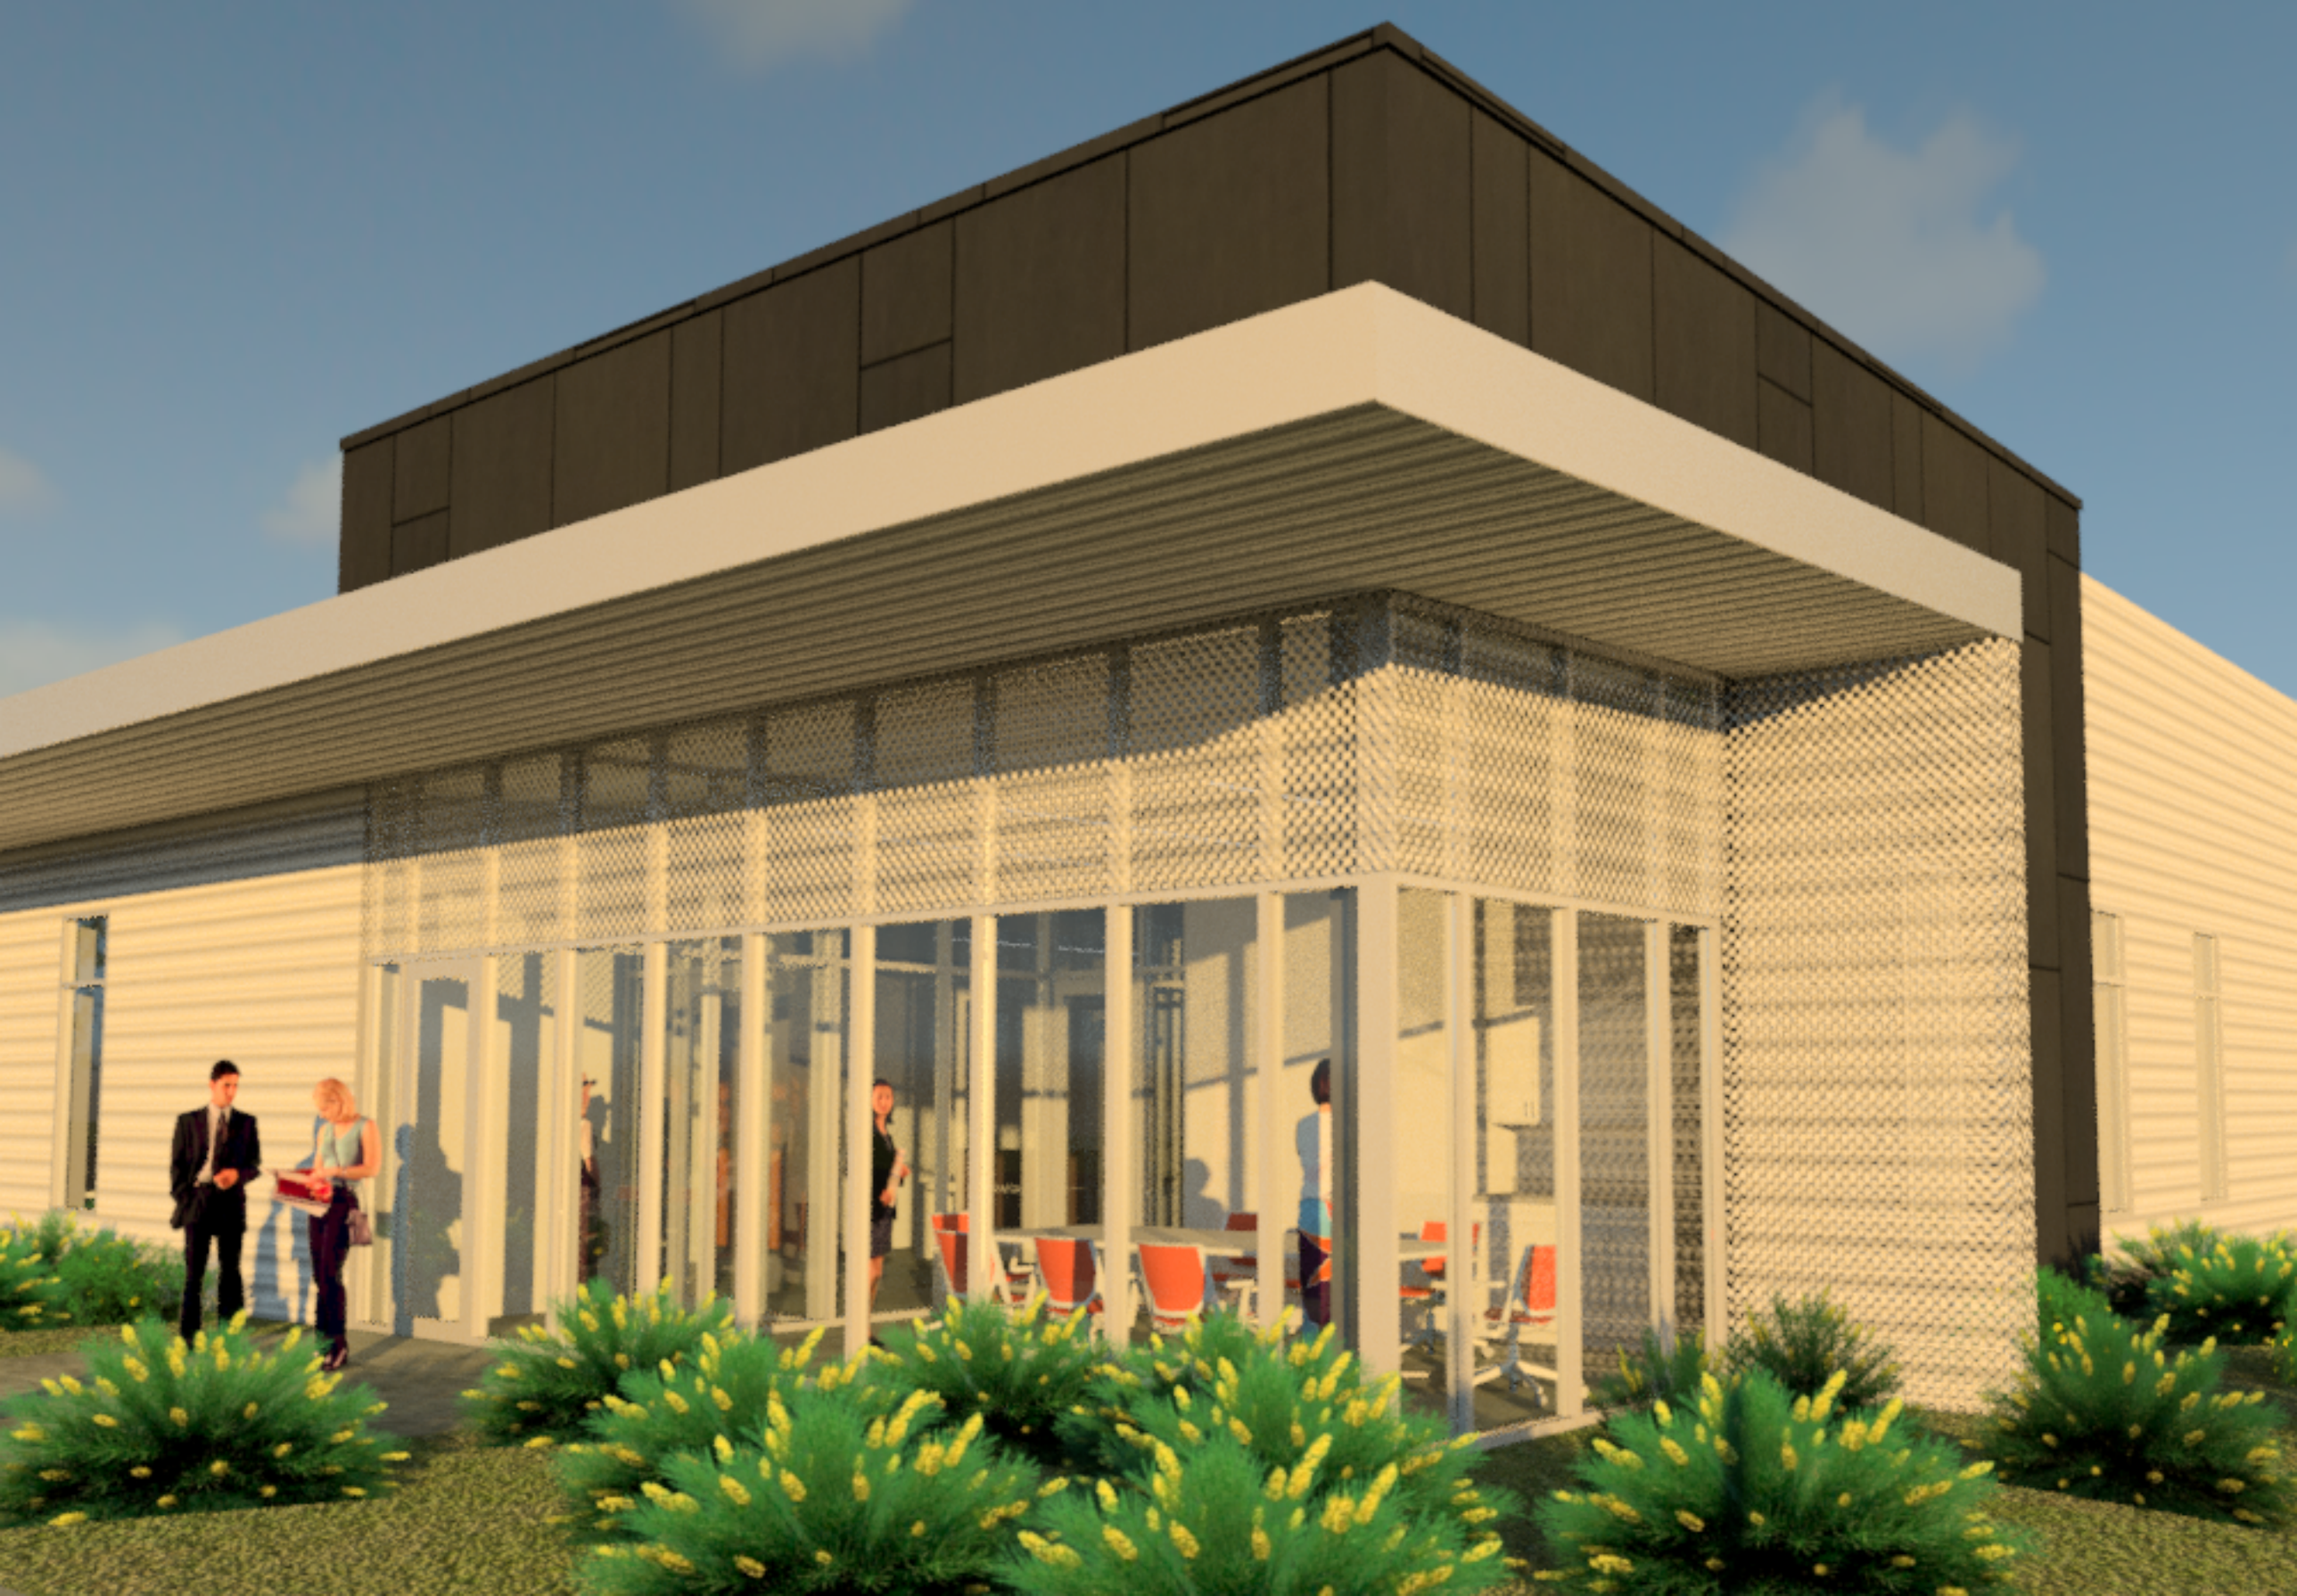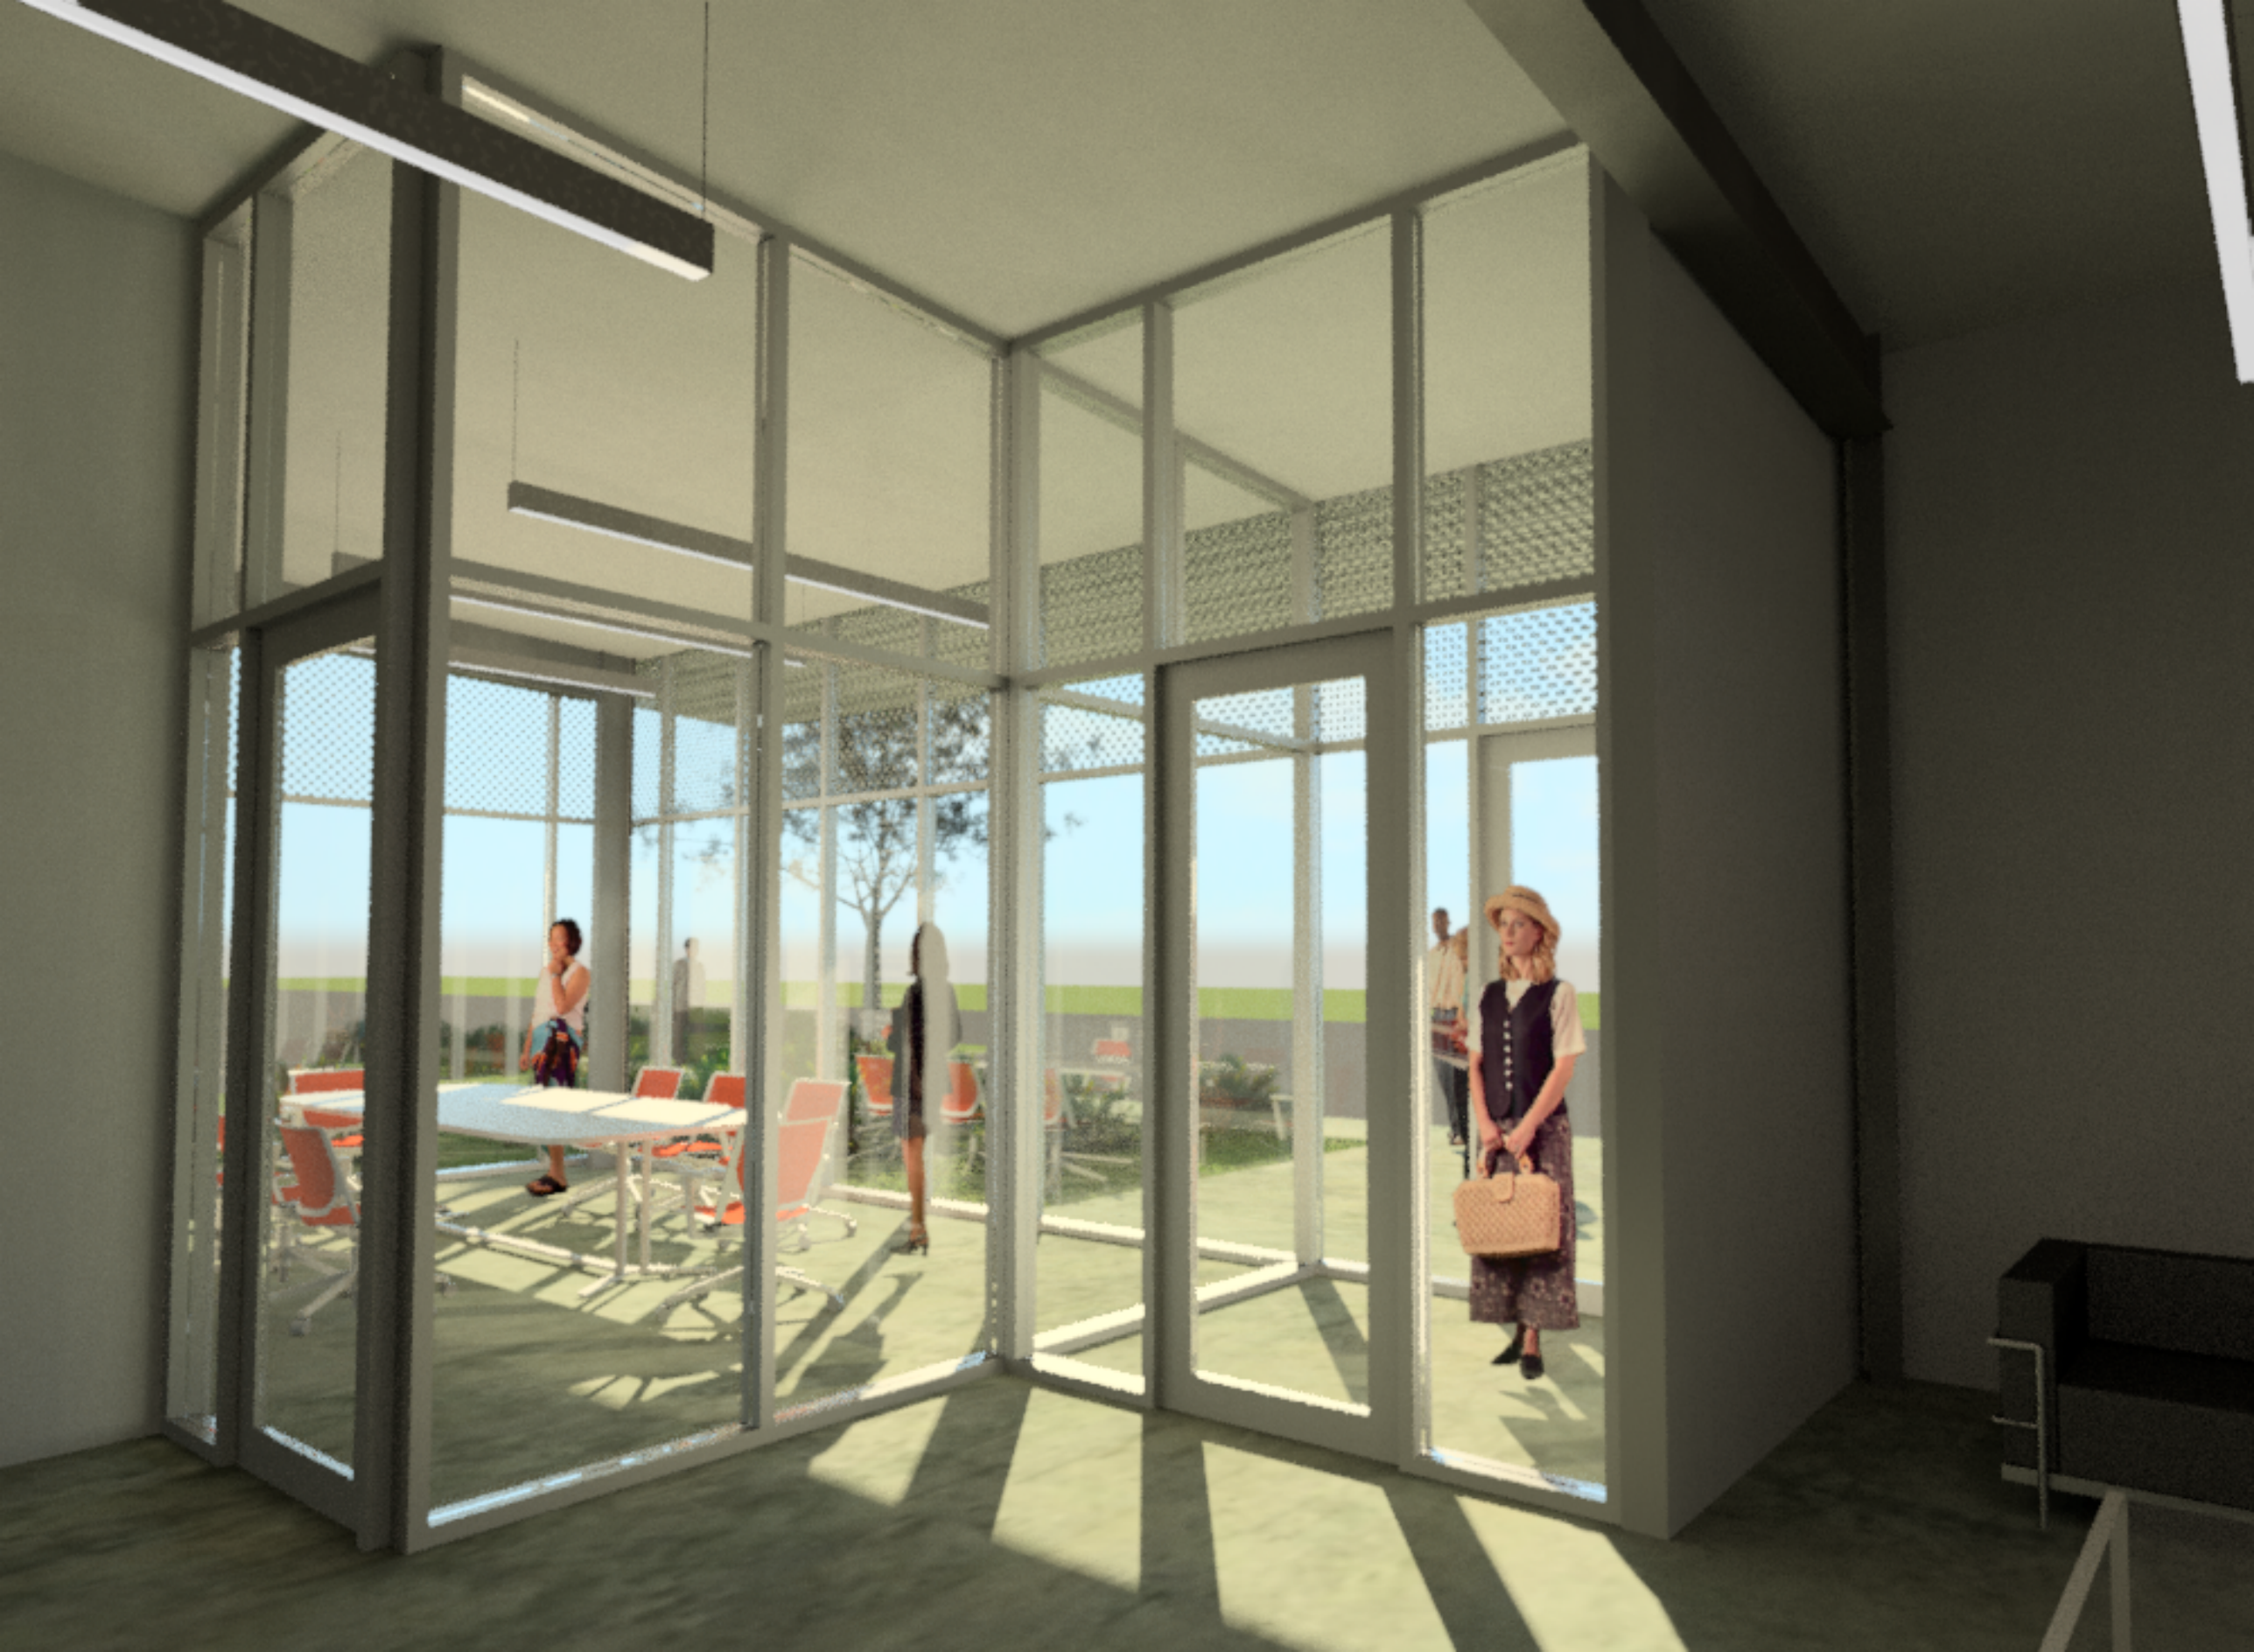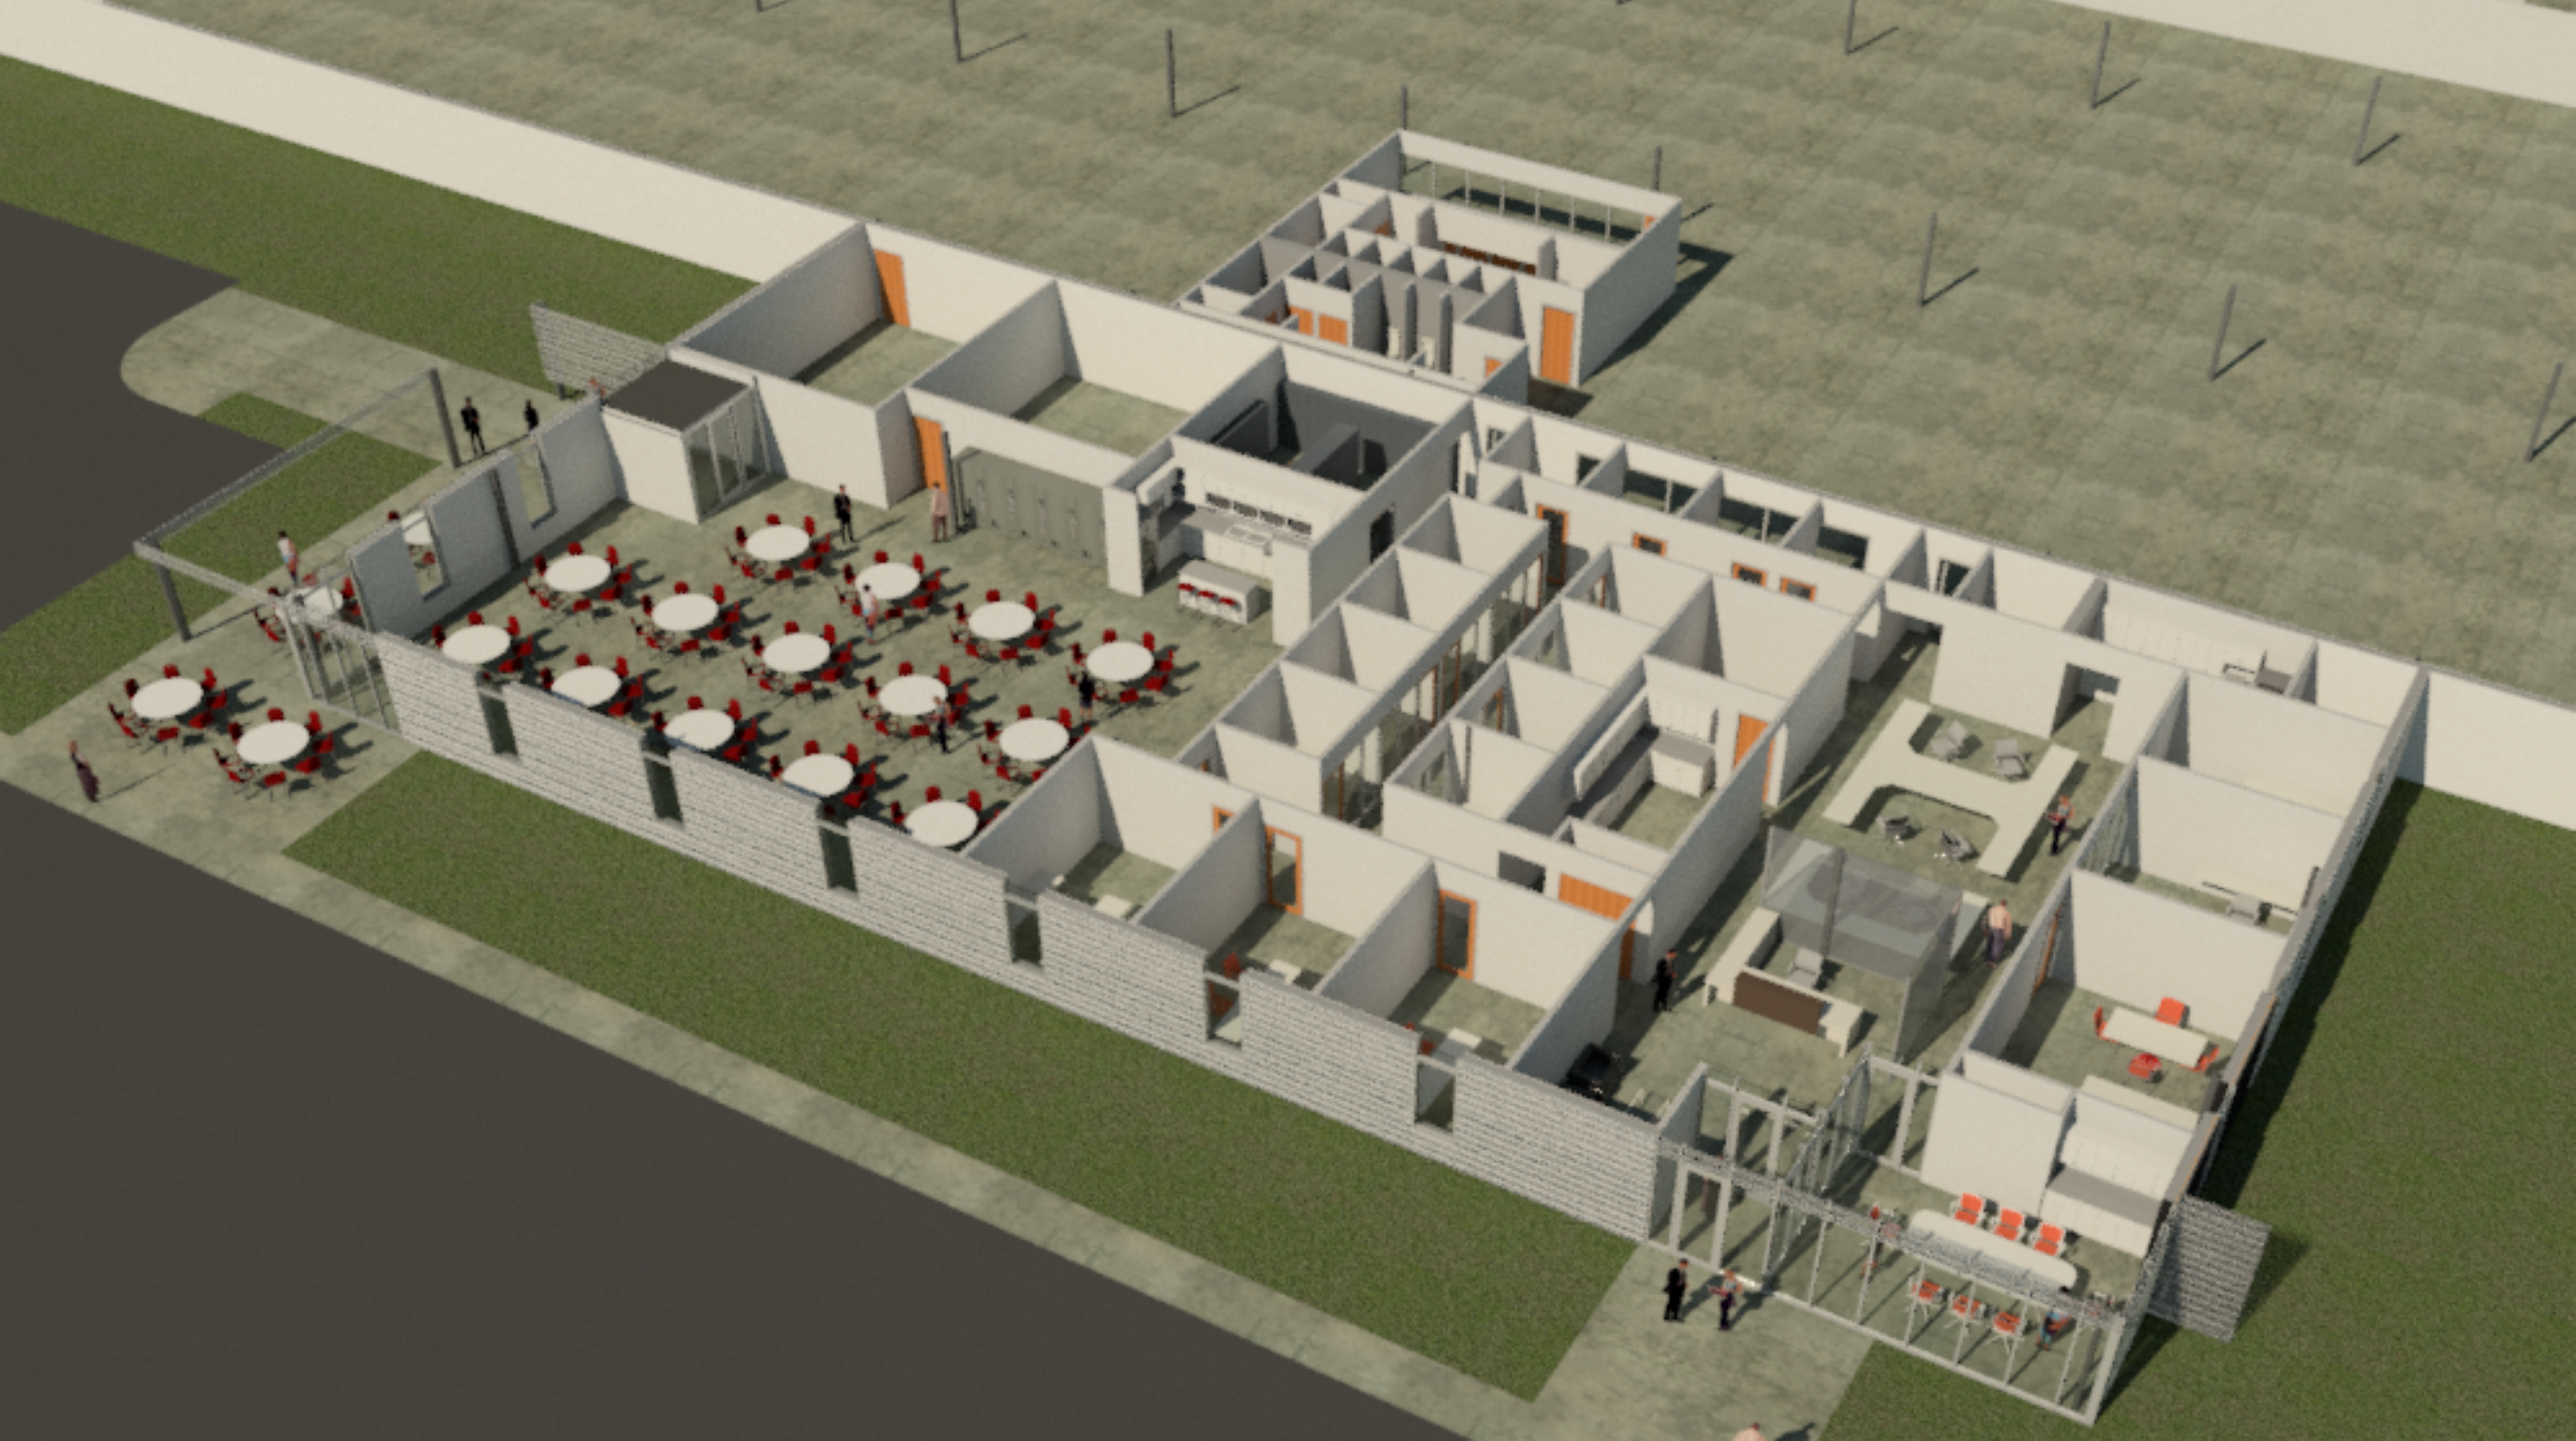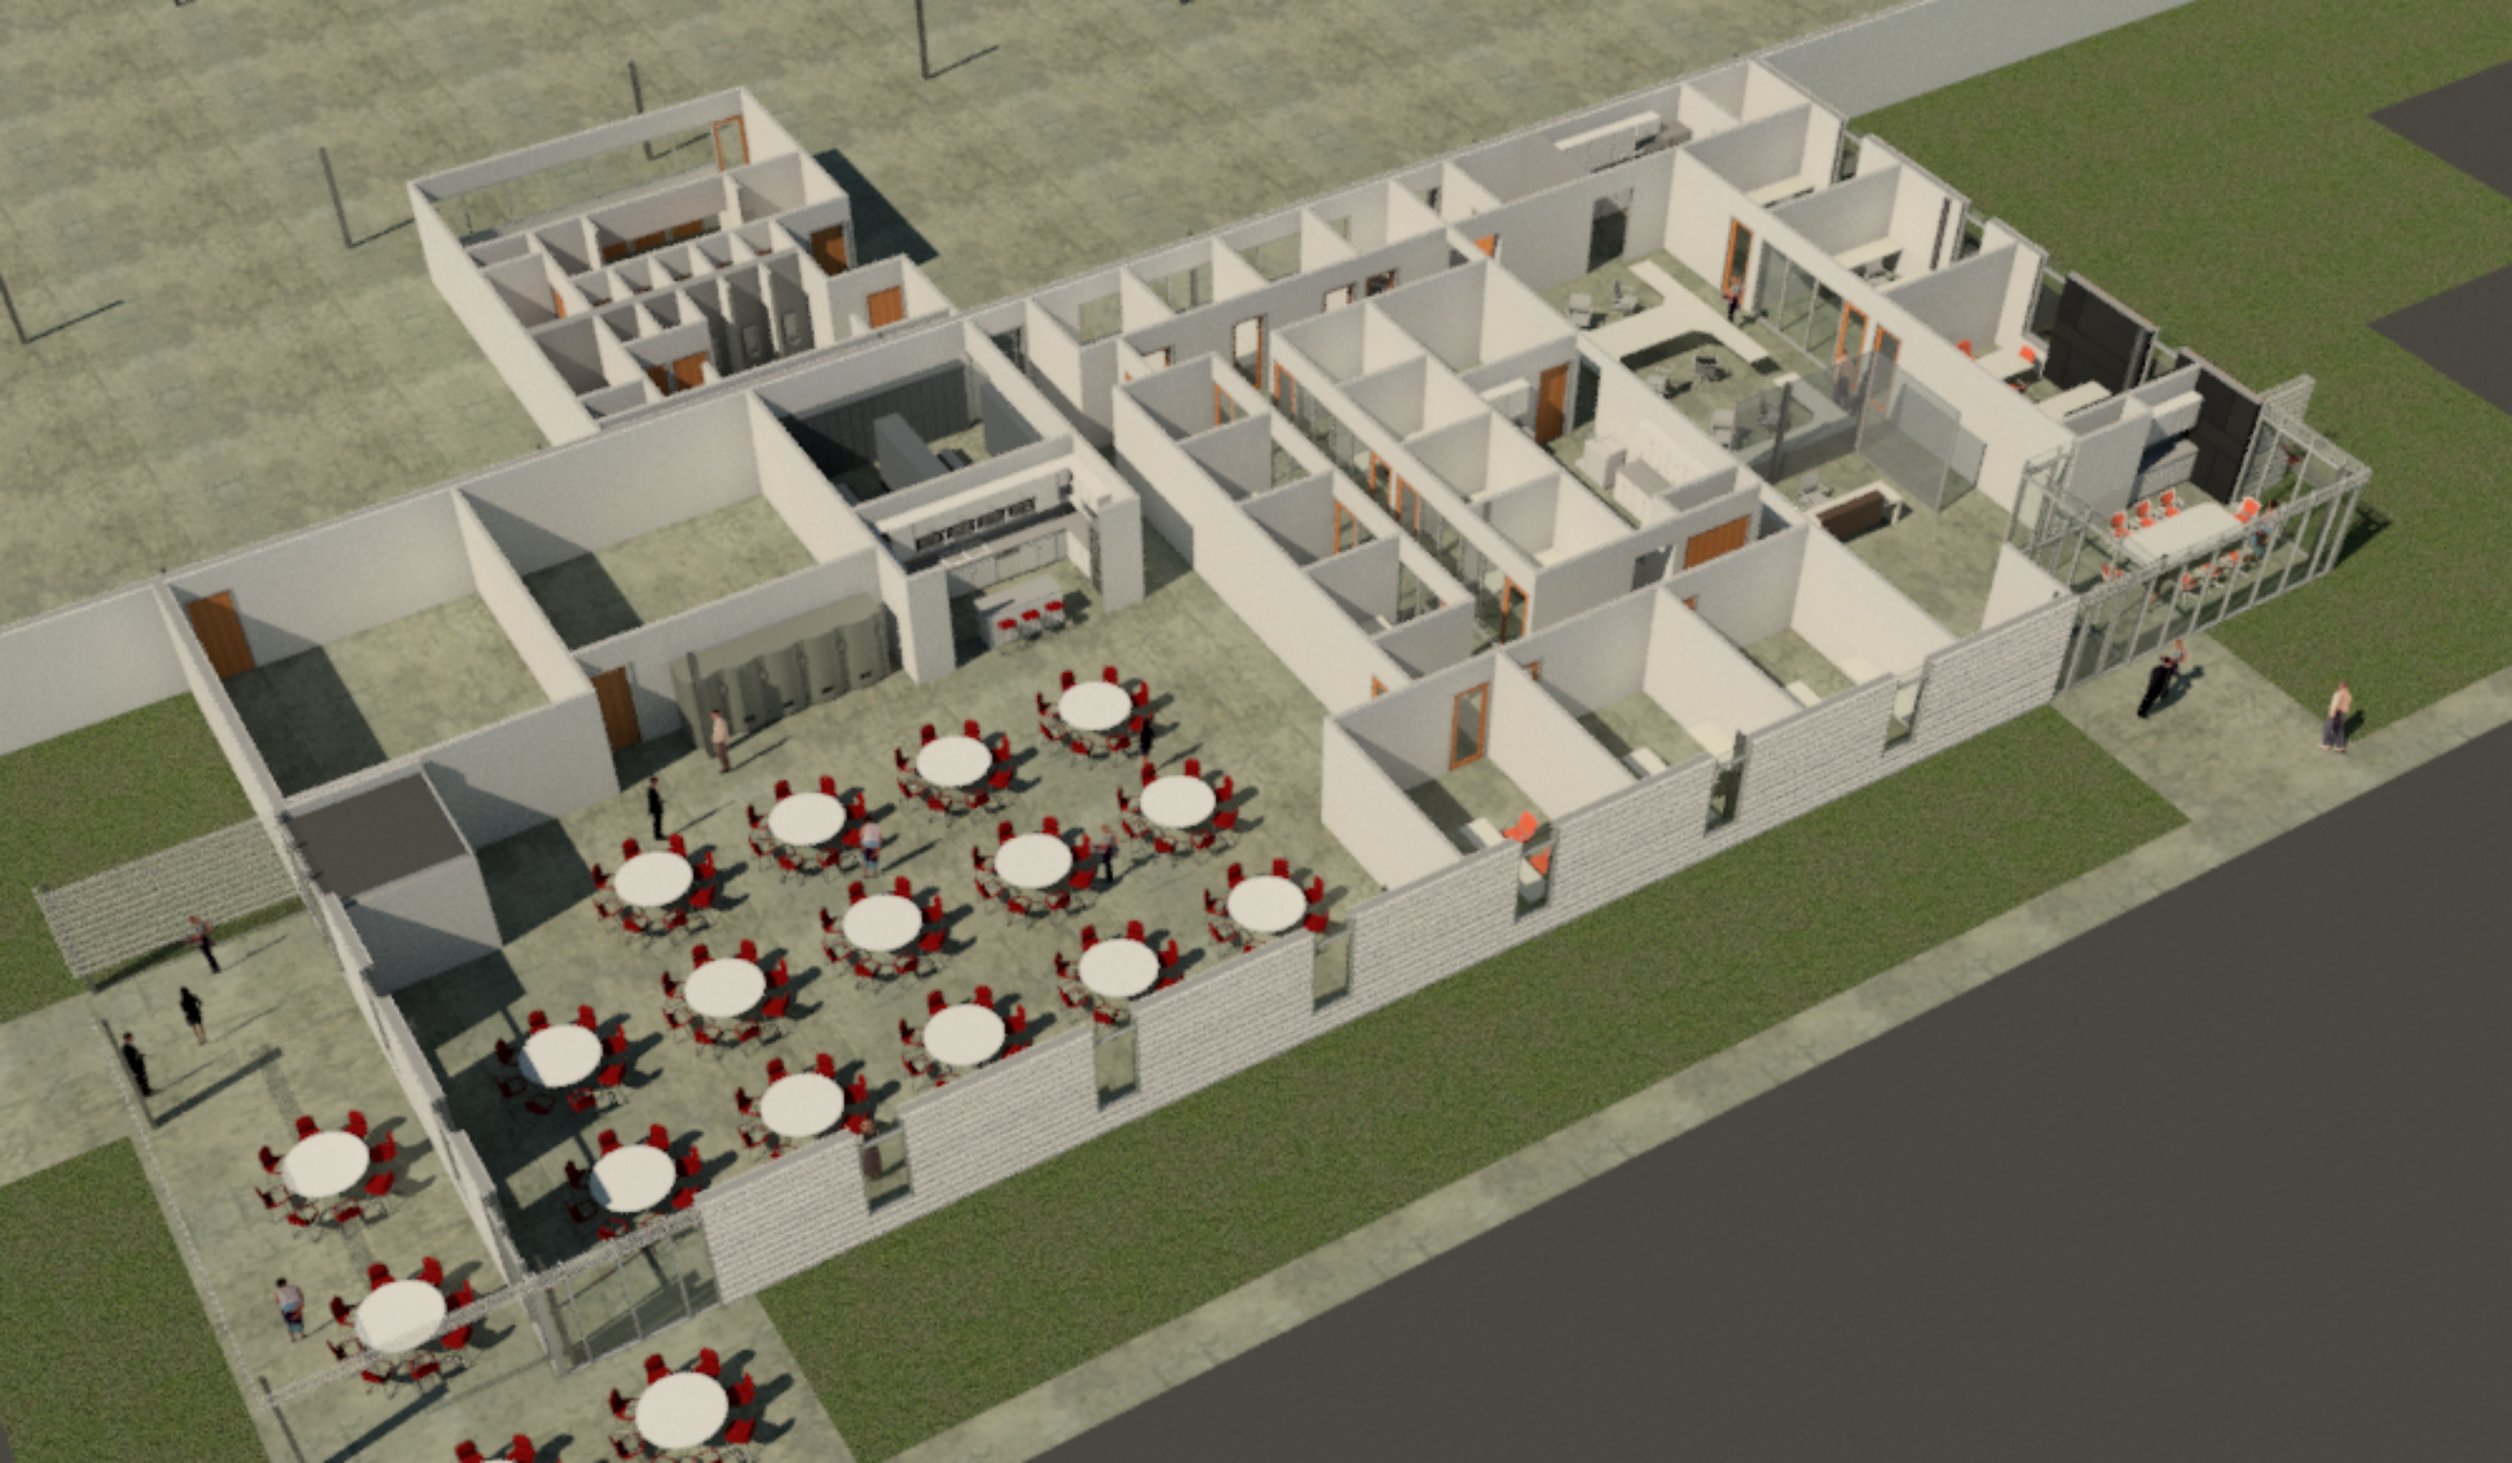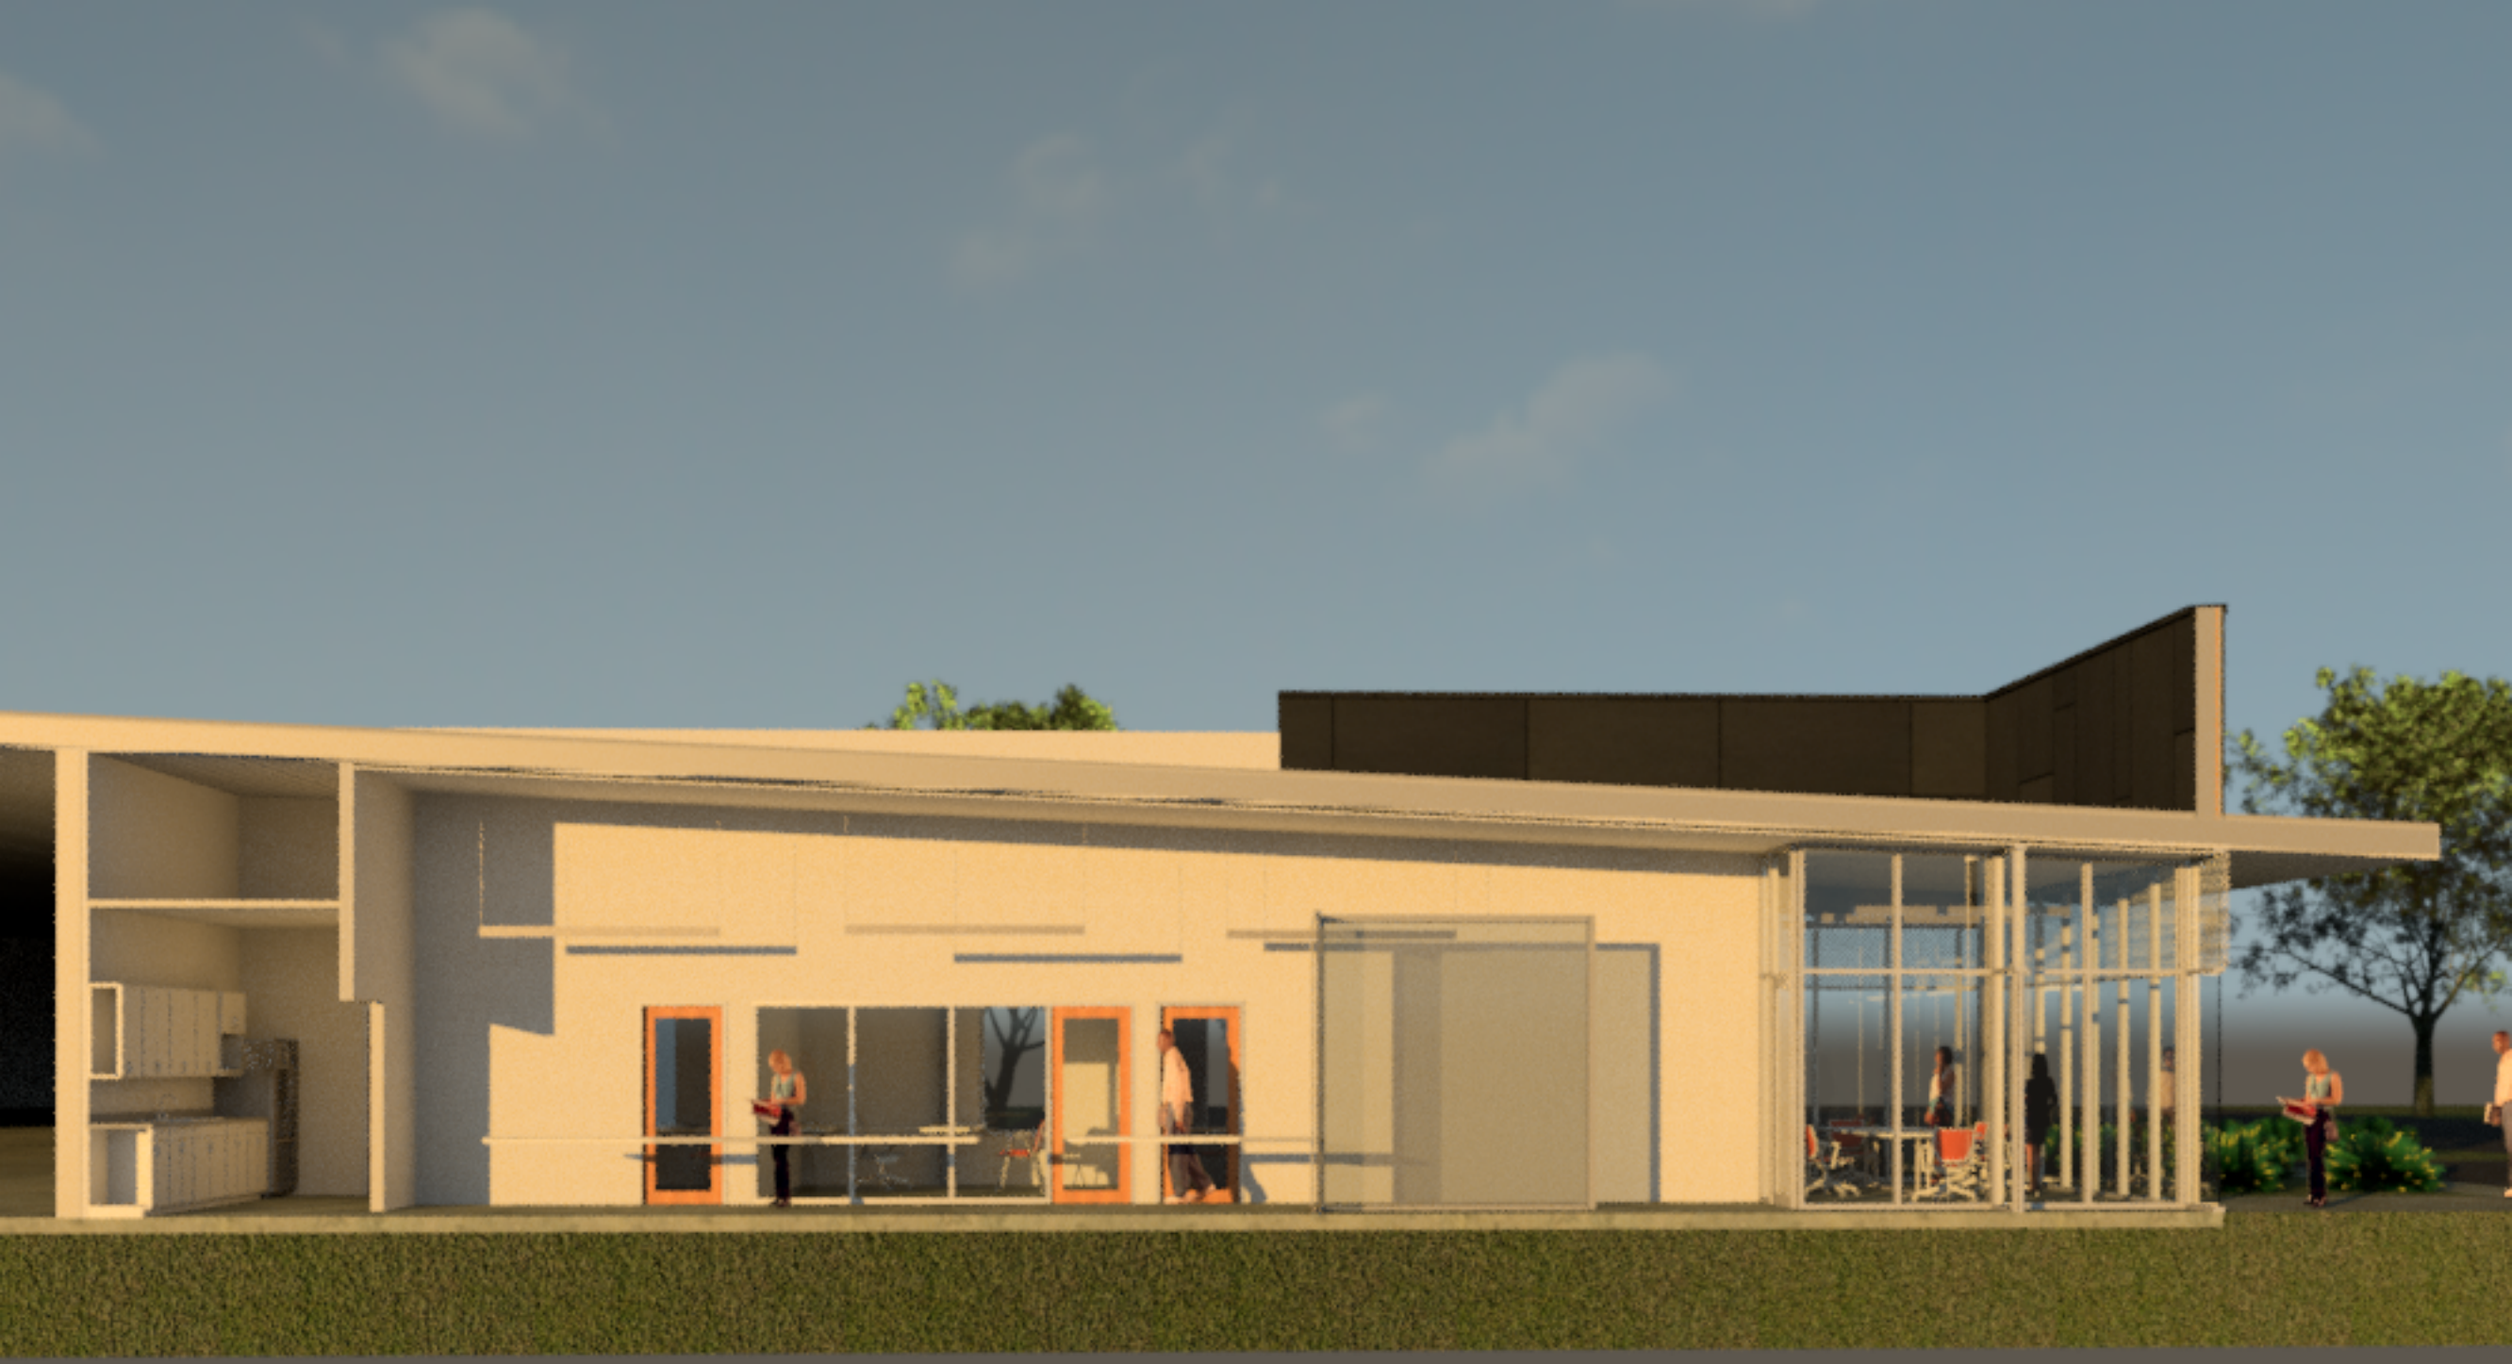
COOLER
WAREHOUSE
KITCHINETTE
OPEN OFFICE
CONFERENCE ROOM